


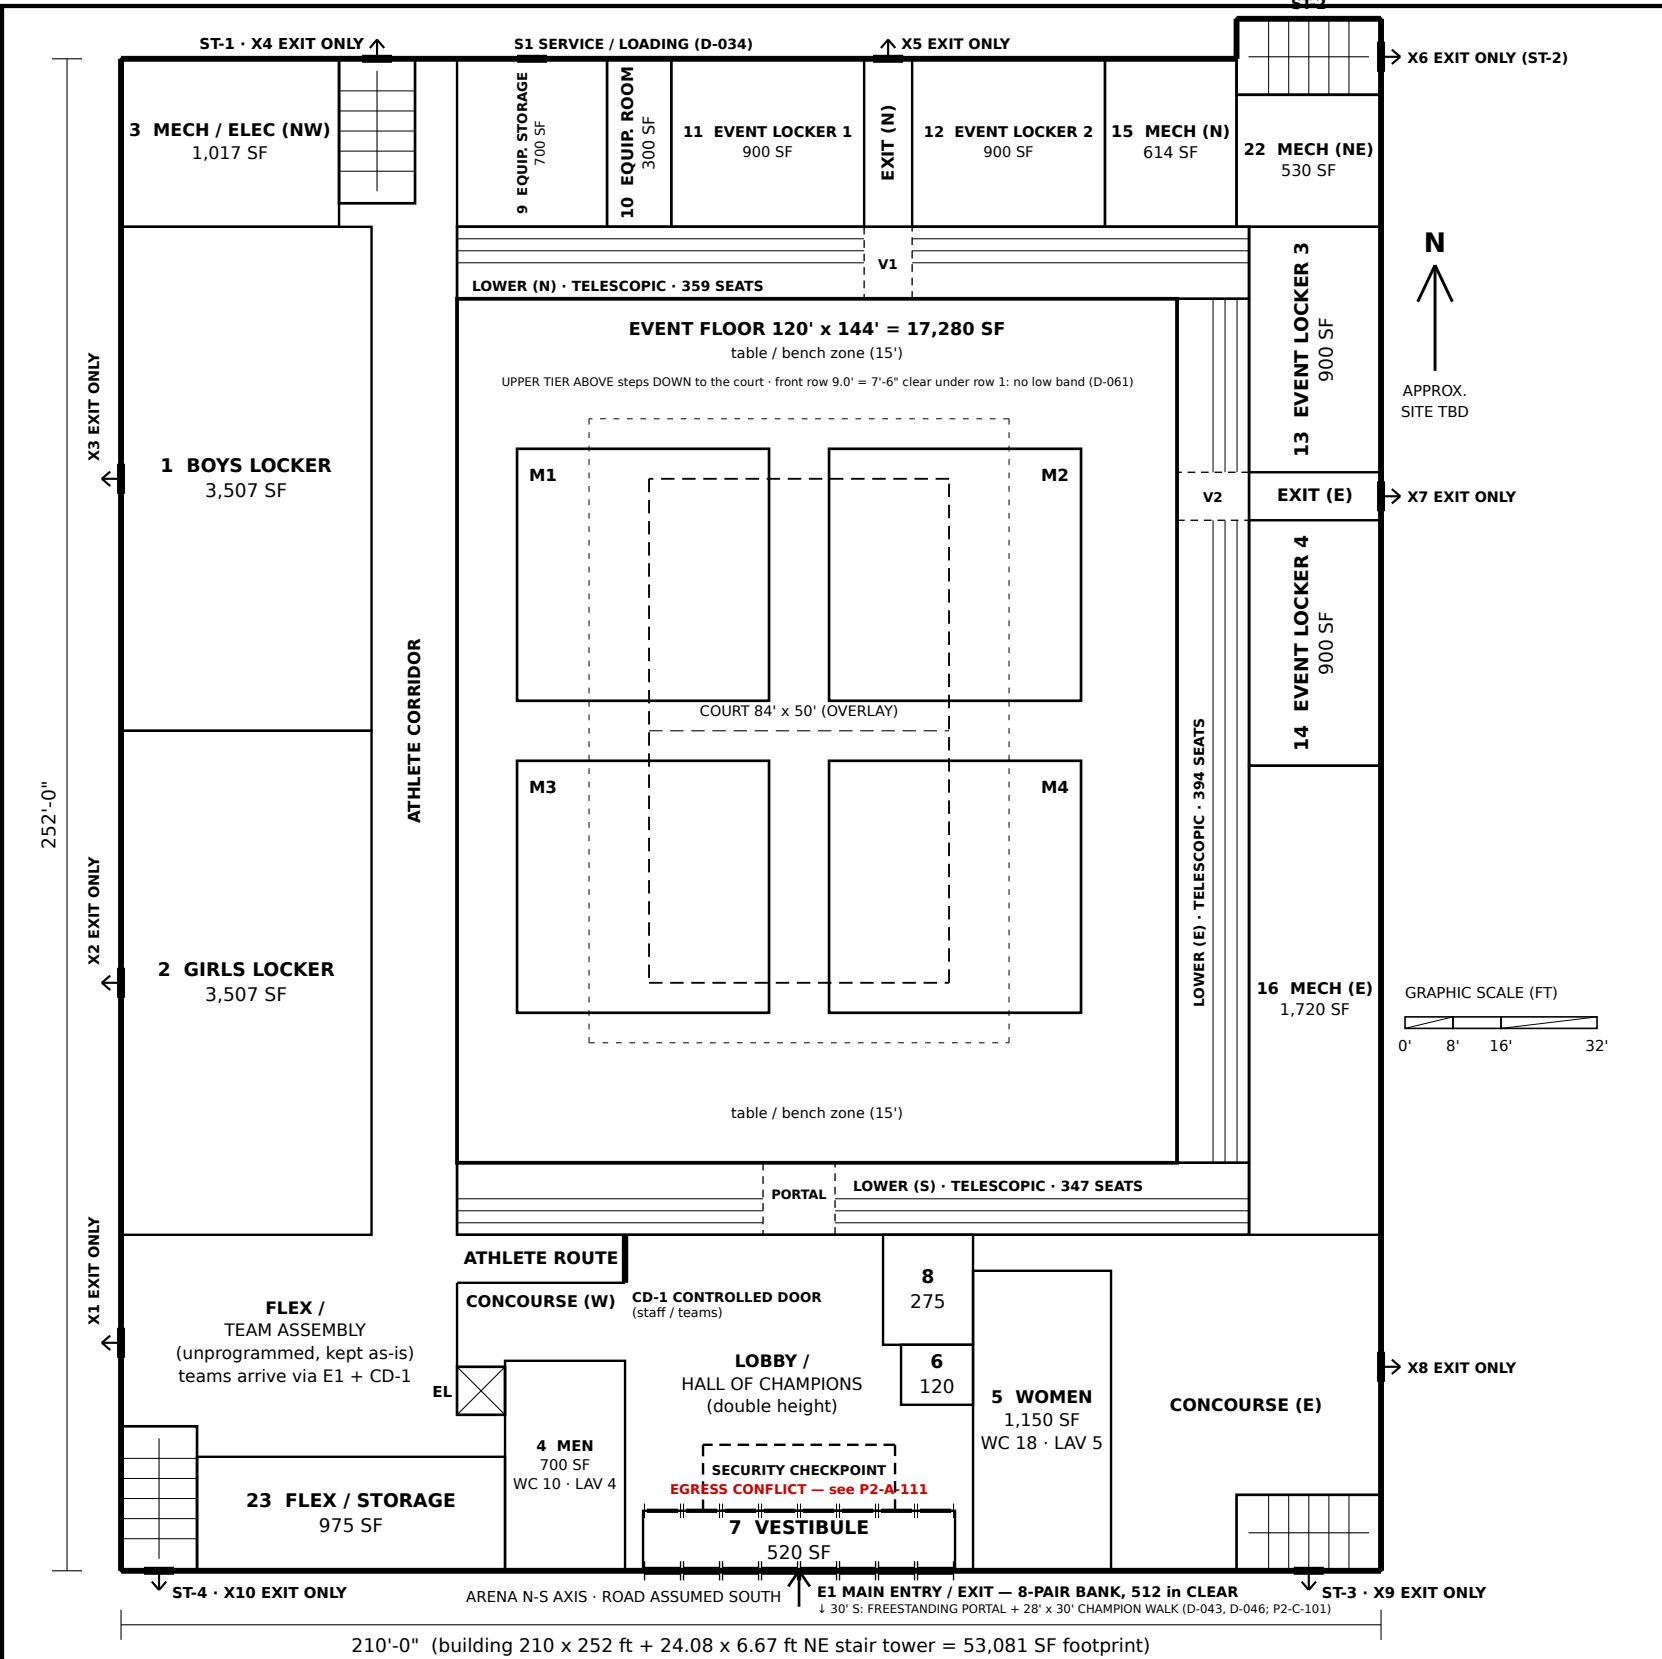

SCHEMATIC — BLOCK PLAN

LEVEL 1 — OVERALL FLOOR PLAN (REV G)

scale 1/32" = 1'-0" on 17 x 11 in · north approximate, road assumed south, site TBD

LEGEND

- Lower tier, TELESOPIC (extended, 6 rows x 24 in; 3.38 SF/seat) — D-009
- 42' wrestling mat (4, 2 x 2)
- 84' x 50' court + 10' runout (overlay)
- Portal / vomitory through the telescopic tier (V1, V2)
- X# = EXIT ONLY — alarmed, no exterior entry hardware (symbol; width not drawn)
- S1 = SERVICE / LOADING door (staff-controlled, not a people entrance; D-034)
- Upper tier above: front row 9.0' = 7'-6" clear, no low band (D-061)
- Security checkpoint zone (size TBD; Rev G: egress conflict, P2-A-111) · CD-1 controlled door
- Room block (tag number + drawn SF)
- Stair (4) / elevator (X), same position on both levels

ROOM SCHEDULE — LEVEL 1 (DRAWN vs PROGRAM side by side, P2-G-003 Rev I; C-3)

| TAG | ROOM                                 | DRAWN SF | PROGRAM | NOTE                                                                          |
|-----|--------------------------------------|----------|---------|-------------------------------------------------------------------------------|
| —   | Event floor + east zone (D-053)      | 17,280   | 17,264  | 120' x 144'; east tier 16 ft from mats                                        |
| —   | Lower tier, telescopic (1,100 seats) | 4,896    | 3,719   | 6 rows; N 359 / S 347 / E 394                                                 |
| 1   | Boys Locker                          | 3,507    | 3,500   |                                                                               |
| 2   | Girls Locker                         | 3,507    | 3,503   | drawn equal to boys (D-013)                                                   |
| 3   | Mech / Elec (NW)                     | 1,017    | 1,063   |                                                                               |
| 4   | Men                                  | 700      | 700     | 14 fixtures (WC 10, LAV 4; urinals ≤ 6 of the WCs)                            |
| 5   | Women                                | 1,150    | 1,150   | 23 fixtures (WC 18, LAV 5)                                                    |
| 6   | First Aid                            | 120      | 120     | Rev G: moved off the south wall for the E1 bank; lobby east side, about 28... |
| 7   | Vestibule                            | 520      | 200     | Rev G: widened to the 52 ft E1 bank (outer + inner bank, 8 pairs each, AS...  |
| 8   | Concession                           | 275      | 275     |                                                                               |
| 9   | Equip. Storage                       | 700      | 700     |                                                                               |
| 10  | Equip. Room                          | 300      | 300     |                                                                               |
| 11  | Event Locker 1                       | 900      | 900     | to the tier line, full 3,600 (D-060): −0                                      |
| 12  | Event Locker 2                       | 900      | 900     | to the tier line, full 3,600 (D-060): −0                                      |
| 13  | Event Locker 3                       | 900      | 900     | to the tier line, full 3,600 (D-060): +0                                      |
| 14  | Event Locker 4                       | 900      | 900     | to the tier line, full 3,600 (D-060): +0                                      |
| 15  | Mech (N)                             | 614      | 642     |                                                                               |
| 16  | Mech (E)                             | 1,720    | 1,797   |                                                                               |
| 22  | Mech (NE)                            | 530      | 554     | NE pocket, up to ST-2 (Rev F: west edge with ST-2, D-061)                     |
| 23  | Flex / Storage                       | 975      | —       | FLEX, unprogrammed, label kept (D-039, C-1)                                   |

AREA CHECK — D-057 (no SF cap, D-056)

|              | DRAWN REV G | REV F  | CHANGE | PROGRAM G-003 I | DRAWN — PROG. |
|--------------|-------------|--------|--------|-----------------|---------------|
| L1 FOOTPRINT | 53,081      | 53,081 | ±0     | 54,415          | −1,335        |
| L2 AREA      | 28,933      | 28,933 | ±0     | 28,186          | +746          |
| TOTAL GSF    | 82,013      | 82,013 | ±0     | 82,601          | −588          |

Floor 120 x 144, east tier 16 ft from the mats. Program = footprint / L2 gross (R-021). Seats N 673 / S 661 / E 866 (Rev F 673 / 661 / 866). Mech 3,881 vs 4,056. Event lockers 3,600 SF (D-060). FLEX kept: team assembly ≈ 2,072, FLEX / STORAGE 975 SF.

ACCESS CONTROL + EGRESS (D-033 DECIDED; layout ASSUMED)

- ONE WAY IN (D-033): E1 → vestibule → security checkpoint (size TBD) → lobby; teams go west through CD-1 to team assembly, athlete corridor, lockers.
- E1 (Shane 11:07 AM CT, Option 1 DECIDED): 8-pair door bank across the lobby's 58 ft south wall, 512 in clear (64 in per pair ASSUMED), inner vestibule bank the same; sized for the standing worst case (466.5 in needed, IBC 1030.2; floor use D-054 OPEN). First aid moved to the lobby's east side (ASSUMED). FINDING: the checkpoint stands in the main-exit path (312 in clear beside it): options on P2-A-111.
- X1-X10 EXIT ONLY: alarmed, no exterior entry hardware, free egress (IBC 2021 1010.2), panic hardware (1010.2.9), no delayed egress in Group A (1010.2.13). Capacities, travel distance, exit separation: P2-A-111. S1 service at the north door (D-034); portal + Champion Walk 30 ft south of E1 (D-043, D-046, D-050; P2-C-101 / P2-A-201).
- D-061 (Option B): Level 2 at 17'-9", 21 in upper risers, front row 9.0 ft: 7'-6" clear under row 1 (≈ 1'-6" structure ASSUMED; IBC 1003.2 minimum, no margin). Exit paths under the tier are clear; no low band, no seats lost.

Sources: phase2.yaml (D-009, D-033-D-035, D-049, D-051-D-054, D-056, D-057, D-060, D-061); Shane 2026-10-04 9:10, 10:27 + 11:07 AM CT; P2-G-002 Rev A, P2-G-003 Rev I, P2-A-111 Rev A; R-007, R-008, R-014, R-015, R-018, R-020-R-022; IBC 2021 Ch. 10 (UpCodes). Geometry: params/phase2\_plan\_rev\_g.yaml.

PRELIMINARY — CONCEPTUAL DESIGN — NOT FOR CONSTRUCTION

|   |         |                                            |                  |                 |     |                                               |          |
|---|---------|--------------------------------------------|------------------|-----------------|-----|-----------------------------------------------|----------|
| PROJECT   | PHASE   | SHEET TITLE                                | SCALE            | DATE            | REV | DRAWN BY                                      | SHEET    |
| Hazel Green Regional Athletic Complex<br>Trojan Horse Arena · Hazel Green area, Madison<br>County, Alabama (site TBD, D-006) | PHASE 2 | OVERALL FLOOR PLAN<br>LEVEL 1 · BLOCK PLAN | 1/32" =<br>1'-0" | October<br>2026 | G   | Drawn by KEYSTONE (AI) for<br>Shane Brazelton | P2-A-101 |