



1 SECTION A-A (NORTH-SOUTH) — looking west

1/32" = 1'-0" · x = 100 (see key plan)

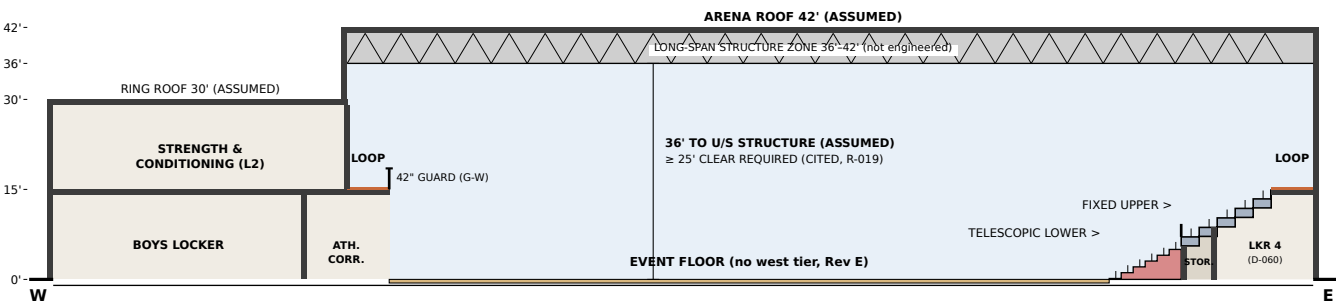


2 SECTION B-B (EAST-WEST) — looking north

1/32" = 1'-0" · y = 150 (see key plan)

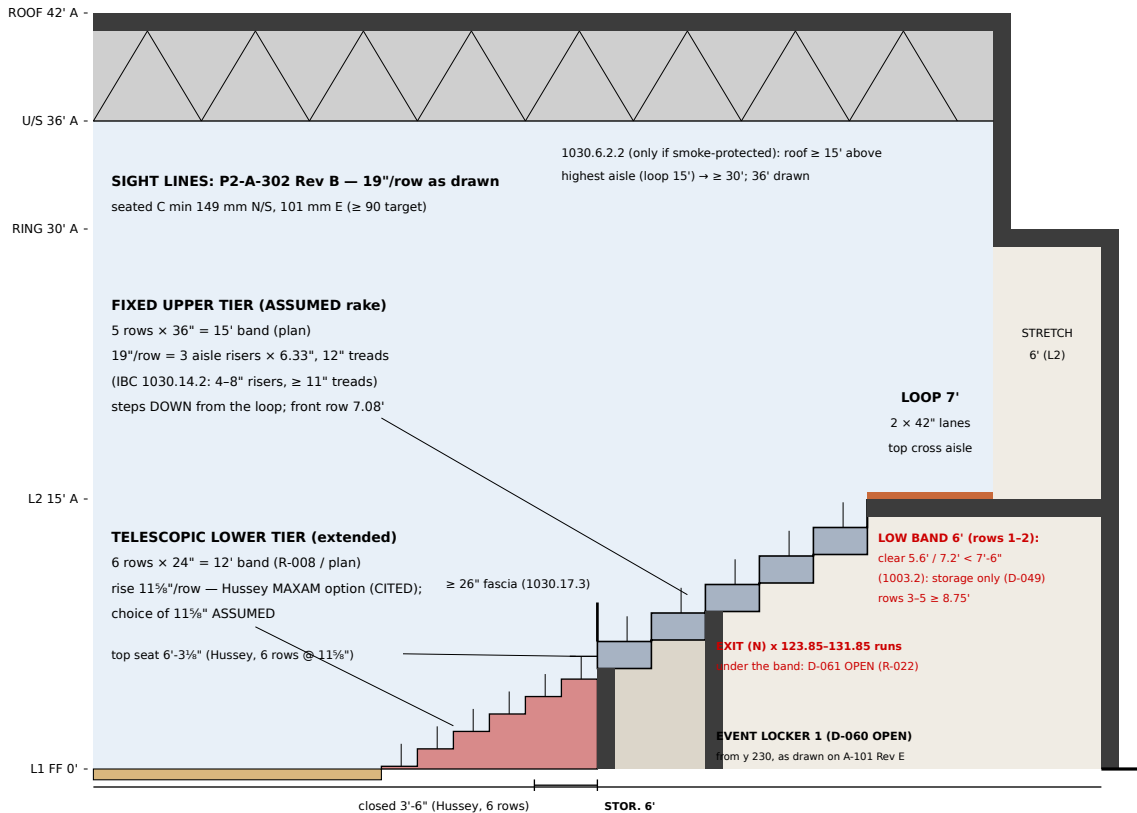


3 NORTH BOWL EDGE (ENLARGED PART OF A-A)

3/32" = 1'-0" · y 196-252 at x = 100

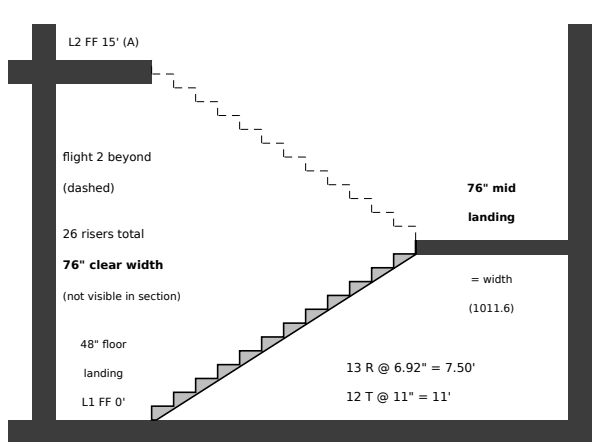


4 TYPICAL EXIT STAIR — 76" CLEAR

1/8" = 1'-0" · 76" mid landing (D-051/052) · 12.67' x 21.33' plan

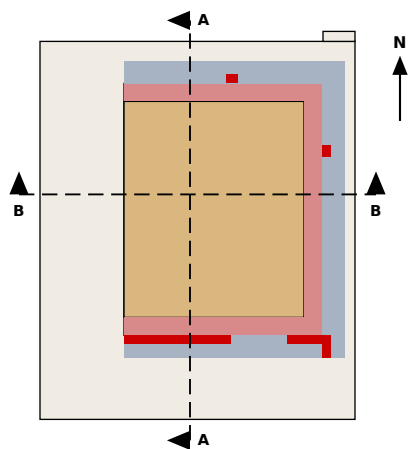

5 KEY PLAN — CUTS

1" = 128' · north up

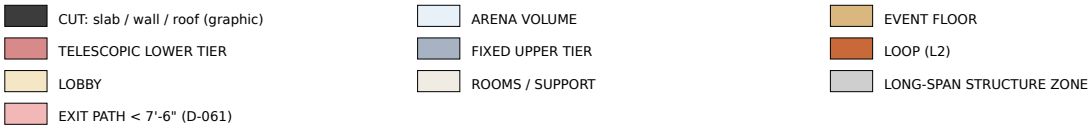

HEIGHTS USED (ft above L1 FF 0'-0")

- L2 FF 15' and ring roof 30' — ASSUMED (R-015). Arena structure underside 36', roof 42' — ASSUMED; $\geq 25'$ clear CITED (R-019).
- Slabs, walls, roof graphic only. Upper-tier deck structure 1.5' under each tread — ASSUMED (sets the low band).

SEATING (P2-A-101 Rev E)

- Lower: telescopic, 6 rows $\times$ 24", 11 $\frac{1}{8}$ " rise (Hussey MAXAM option, CITED; choice ASSUMED); east front 16' from the nearest mat (D-053); building 210' wide.
- Upper: fixed, 15' band, 5 rows $\times$ 36", 19"/row (D-053 DECIDED) = 3 aisle risers $\times$ 6.33", 12" treads (1030.14.2); steps DOWN from the loop (D-049) to a 7.08' front row.
- UNDER THE UPPER TIER (D-049; D-060 OPEN, drawn as on A-101 Rev E): stepped soffit gives 5.6' / 7.2' clear under rows 1-2 = 6' LOW BAND < 7'-6" (1003.2): under-tier storage / stack only. Rows 3-5: 8.75'-11.9'. Event lockers start behind the band (2,723 SF vs 3,600).
- SIGHT LINES: P2-A-302 Rev B (as drawn): seated C min 149 mm N/S, 101 mm E; standing 127 / 72 mm.

EXIT-PATH CONFLICT — D-061 OPEN (R-022)

- Paths under the low band have < 7'-6": Exit N 8', Exit E 8', SE concourse 38' (23' S + 15' E), lobby / portal / athlete-route edge 71' (x 56-127). Red on A-A and the key plan. NOT redesigned.

D-061 OPTIONS (R-022)

- A — omit upper rows 1-2 over the paths: -125 seats (8 + 8 + 38 + 71); upper 1,155 $\rightarrow$ 1,030 = 70 short of 1,100. Rail off the non-path strips instead: -56 (N 8, E 8, portal 12, athlete route 28) $\rightarrow$ 1,099, 1 short.
- B — raise L2 / loop / upper tier to 17'-9" with 21" risers (front row 9.0', $\geq 7'$ -6" clear): 0 seats lost; lockers back to 3,600 SF; stairs 31 R, +34.8 SF each per level ($\approx$ +279 SF); ring roof 32.75'; C unchanged.

GUARDS

- Loop open edges G-W (x = 56) and G-S (y = 34): 42" (IBC 2021 1015.2 / 1015.3). Upper-tier front fascia $\geq 26"$ (1030.17.3), 36" at aisle feet (1030.17.4).

STAIRS (ST-1..ST-4)

- 76" clear (D-052 DECIDED). 26 R @ 6.92", 2 flights of 13, 11" treads (1011.5.2); 76" intermediate landing = width (1011.6, D-051); 48" floor landings. Per stair 12.67' $\times$ 21.33' = 270.2 SF per level, as drawn on A-101/102 Rev E.

ROOF HEIGHT (1030.6.2.2, if smoke-protected)

- Roof $\geq 15'$ above the highest aisle (loop 15') $\rightarrow \geq 30'$; 36' drawn.

CUTS

- A-A: x = 100, looking west. B-B: y = 150, looking north. Geometry from P2-A-101/102 Rev E. Colors graphic only; 'A' = ASSUMED.

PRELIMINARY — CONCEPTUAL DESIGN — NOT FOR CONSTRUCTION

PROJECT	PHASE	SHEET TITLE	SCALE	DATE	REV	DRAWN BY	SHEET
Hazel Green Regional Athletic Complex Trojan Horse Arena · Hazel Green area, Madison County, Alabama (site TBD, D-006)	PHASE 2	BUILDING SECTIONS SCHEMATIC · COLOR	AS NOTED	October 2026	C	Drawn by KEYSTONE (AI) for Shane Brazelton	P2-A-301