



(a) WRESTLING — 4 x 42' MATS, 2 x 2

1" = 50'-0" · tier open · NFHS clearances all PASS (table at right)

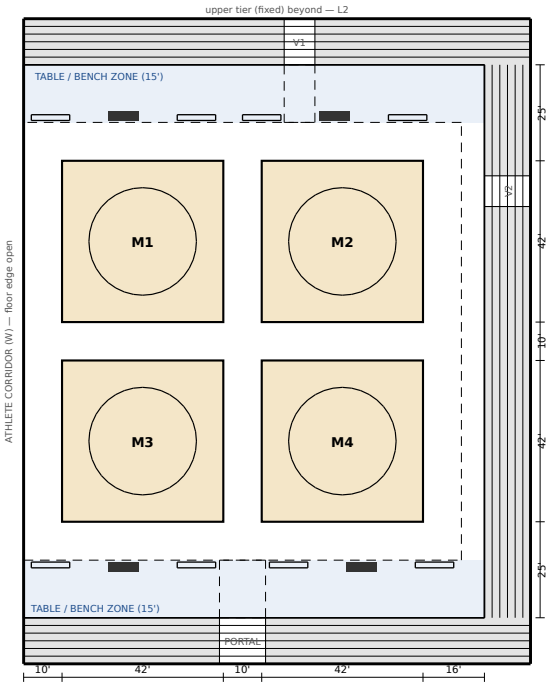


(c) TELESCOPIC LOWER TIER — OPEN vs CLOSED

1" = 50'-0" · 6 rows x 24 in = 12' open; 3'-6" closed (Hussey)

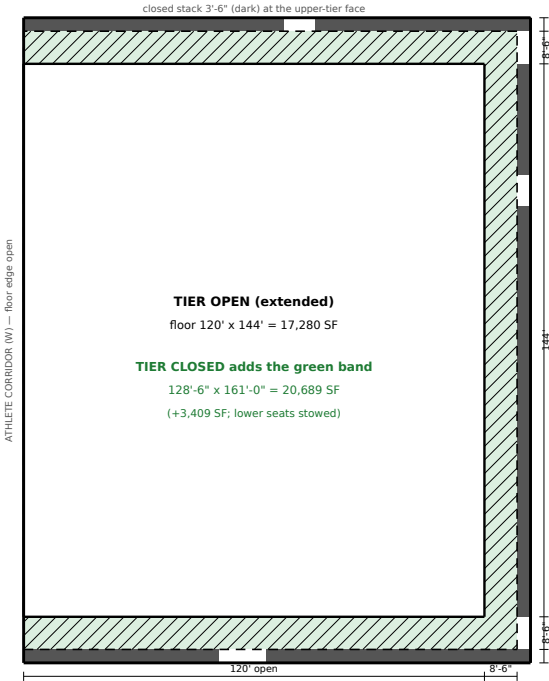


(b) BASKETBALL — 1 COURT (IN PARAMS)

1" = 50'-0" · tier open · mats up, court down, seats stay

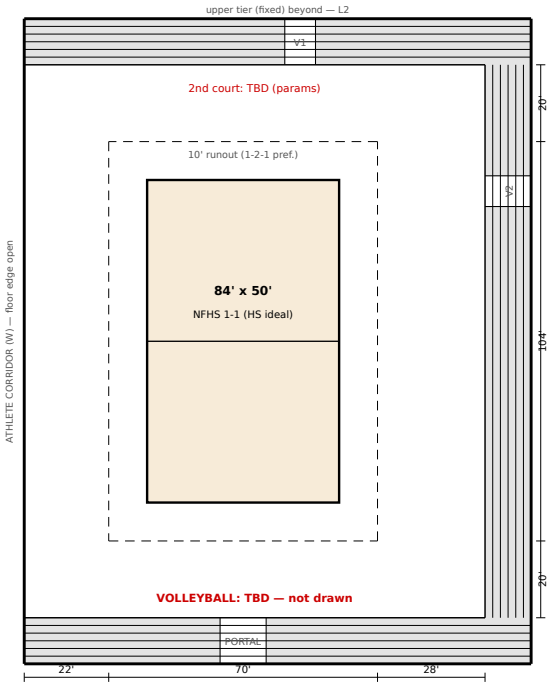

(d) EVENT-FLOOR CASES — P2-G-002 Rev A

1" = 100'-0" · hatched 114' x 144' = 16,416 SF · D-054 OPEN

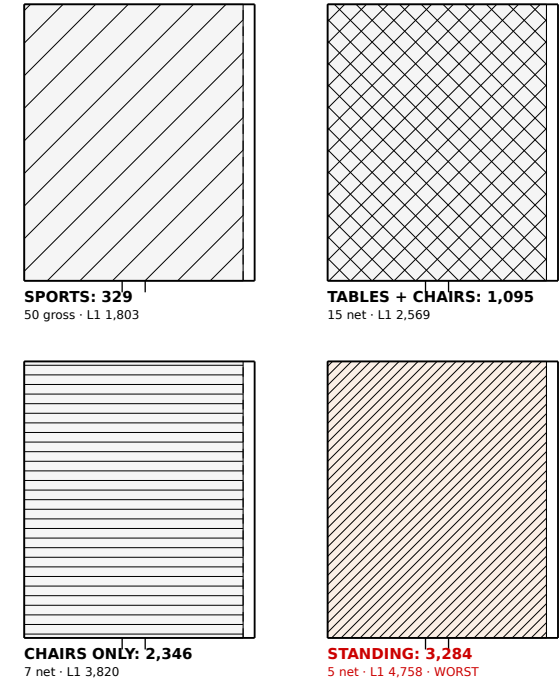

(a) WRESTLING — NFHS CLEARANCES ON THIS LAYOUT

RULE	ITEM	REQUIRED	DRAWN	
NFHS 2-1-2	Circle + safety area	$\geq 28 + 2 \times 5 = 38$ ft	42 ft mat (7 ft each side of a 28 ft circle)	PASS
NFHS 2-1-5	Space around each mat	≥ 10 ft	W 10 · between 10 / 10 · E 16 · S / N 25 / 25	PASS
NFHS 2-3	Scorer's table to mat	≥ 10 ft	10.5 ft	PASS
NFHS 2-1-5	Bench to mat / to table	≥ 10 / ≥ 10 ft	10.5 / 10 ft	PASS
KHSAA (rec.)	Circle to walls / tier	about 10 ft	W 17 (open to corridor) · E 23 · S / N 32 / 32	PASS

Tables 8' x 2.5' and benches 10' x 1.5' ASSUMED (no size in NFHS text found), front edge 10.5' from the mat. Portal and V1 aisles kept clear (egress, P2-A-111). Tournaments: up to two team personnel in chairs at the mat edge (NFHS 2-2-2); dual meets can use one mat (R-005.5). Rule text: NFHS 2014-15 (R-005); current book UNVERIFIED. 28' circle drawn = NFHS minimum (42' mats are often sold with a 32' circle).

(b) BASKETBALL / VOLLEYBALL — FROM PARAMS ONLY

1 court (phase2.yaml basketball_full_courts: 1): 84' x 50' (NFHS 1-1) + 10' runout (1-2-1: $\geq 3'$, 10' preferred) = 70' x 104'; to the floor edge W 22' / E 28' / S 20' / N 20'. Clear height $\geq 25'$ (R-019). Boundary + division line only (other markings not drawn: not researched); team benches / scorer's table for basketball: TBD (not in params or decisions).

VOLLEYBALL: TBD — phase2.yaml volleyball_courts: TBD; R-012 volleyball not researched. Nothing drawn (no new program). 2nd basketball court: TBD (phase2.yaml basketball_second_court: TBD; 'only after clear span is measured').

(c) TELESCOPIC LOWER TIER — FLOOR ZONES

STATE	FLOOR ZONE	SF	LOWER SEATS
Open — extended 12' (6 x 24 in)	120' x 144'	17,280	1,100
Closed — 3'-6" stack	128'-6" x 161'-0"	20,689	0
Gain (N, S, E)	+8'-6" each side	+3,409	

Stack closes against the upper-tier face line (N y = 224, S y = 56, E x = 188): P2-A-302 Rev C keeps the stack in front of the upper-tier face, not recessed (open rows 5-6 would sit under < 7'-6"). Each side (N, S, E) operates on its own (ASSUMED; banks and motorization TBD, manufacturer). Folding and telescopic seating that is not a building element: ICC 300 (IBC 2021 1030.1.1). Spaces under bleachers: 1-hour separation unless an exception applies (1030.1.1.1) — architect. Portal, V1, V2 stay open through the stack.

CONVERSIONS (ASSUMED SEQUENCE)

- Wrestling: tier open; mats roll in from EQUIP. STORAGE at the top of the athlete corridor (plan Rev G; S1 service door, D-034).
- Basketball: mats up and stored, court surface down (surface type TBD); seats stay (phase2.yaml floor_converts).
- Floor events (D-054 OPEN): tier open or closed per event; chairs, tables, stage / platform and their storage are NOT in the program (TBD) — no room drawn for them.
- Occupant load posted per configuration (IBC 1004.9); the building official assigns the loads.

Schematic overlays for the owner, the architect of record and the AHJ. Not a code review and no statement of approval (D-008). Sports rules quoted from older NFHS editions (current books paywalled): UNVERIFIED against the current edition. Furniture positions ASSUMED.

(d) EVENT-FLOOR OCCUPANCY CASES — D-054 OPEN

CASE	FACTOR	FLOOR	L1	LAYOUT NOTE
Sports	50 gross	329	1,803	Mats (a) or court (b) on the floor; tier open. Exercise 50 gross ASSUMED for sports use (AHJ assigns).
Tables + Chairs	15 net	1,095	2,569	Tables + chairs: aisle widths measured 19 in from the table edge (1030.13.1); level aisles 42 in (seats both sides) / 36 in (one side) (1030.9.1). Table layout TBD.
Chairs Only	7 net	2,346	3,820	Chairs in rows: ≥ 12 in clear between rows up to 14 seats, + 0.3 in per seat beyond 14 (backrests), ≤ 100 seats per row with aisles both ends (1030.13.2, 1030.13.2.1). Row plan TBD.
Standing	5 net	3,284	4,758	Open floor, no stage drawn (stage / platform TBD, D-054). Worst case: L1 exits sized for it (P2-A-111 Rev A); restrooms short (D-064 OPEN).

Floor = 16,416 SF (G-002, 114' x 144'; hatched from the W edge, the east 6' strip of the drawn floor, D-053, unhatched); L1 = floor + 1,100 lower seats + 374 other L1 rooms. Sensitivity: whole drawn zone 17,280 SF standing = 3,456 (L1 4,930; E1 479.4 in still under 512, P2-A-111). Tier CLOSED: standing 4,138 / chairs 2,956 on 20,689 SF with no lower seats → L1 4,512 / 3,330, below the 4,758 design case the L1 exits were sized for (arithmetic; net = gross ASSUMED). Post the occupant load for each intended configuration near the main exit (IBC 2021 1004.9).

OPEN DECISIONS — NOT ASSUMED HERE

- D-054: Floor uses beyond sports (concerts, graduations, expos): OPEN — cases shown for planning only.
- D-064: Restrooms at the worst case: OPEN.
- D-065: Checkpoint vs egress: OPEN.
- D-066: Exit discharge from E1 vs the 28 ft walk / arch: OPEN.

Floor uses beyond sports wait on Shane (D-054). L1 exits are already sized for the standing worst case (Shane 11:07 AM CT, P2-A-111 Rev A); restroom fixtures for it are not (D-064).

LEGEND

Grey band = telescopic lower tier open (thin lines = 24 in rows) · dark band = closed stack · tan = mat (circle = 28' NFHS minimum) · black bar = scorer's table · open bar = team bench · blue = table / bench zone · dashed = 10' mat area / keep-clear aisle / runout · green hatch = floor gained when closed · hatch styles (d): wide = sports, cross = tables, horizontal = chairs, dense = standing.

Sources: params/phase2_overlays.yaml; phase2_plan_rev_g.yaml; phase2_code.yaml; R-005 (NFHS Wrestling 2-1-2, 2-1-5, 2-2-1, 2-2-2, 2-3; KHSAA); R-012 (NFHS Basketball 1-1, 1-2-1); R-019; R-008 / Hussey MAXAM; R-007.2 (IBC 2021 T1004.5); IBC 2021 1004.9, 1030.1.1, 1030.1.1.1, 1030.9.1, 1030.13.1, 1030.13.2, 1030.13.2.1 (UpCodes, retrieved 2026-10-04); P2-G-002 Rev A; P2-A-111 Rev A; P2-A-302 Rev C; D-009, D-014, D-030, D-053, D-054; Shane 2026-10-04 11:45 AM CT.

PRELIMINARY — CONCEPTUAL DESIGN — NOT FOR CONSTRUCTION

PROJECT Hazel Green Regional Athletic Complex Trojan Horse Arena · Hazel Green area, Madison County, Alabama (site TBD, D-006)	PHASE PHASE 2	SHEET TITLE FLOOR OVERLAYS MATS, SEATING + CONVERSIONS	SCALE AS NOTED	DATE October 2026	REV A	DRAWN BY Drawn by KEYSTONE (AI) for Shane Brazelton	SHEET P2-A-103
--	-------------------------	--	------------------------------	---------------------------------	-----------------	---	--------------------------