

SCHEMATIC — BLOCK PLAN, CONCEPT ENVELOPE

LEVEL 2 — OVERALL FLOOR PLAN (REV H)

Rev G (approved, D-080) with ST-2 as the 29 ft drum of P2-A-101 Rev L (D-081). Rooms, tiers, guards, seat counts and the R 13 NE loop corner are Rev G unless listed under CHANGES. Rev G tower shown dashed.

CHANGES FROM REV G (all ASSUMED)

- ST-2: 29 ft drum centred (182, 262.5), same as Level 1; holds the 12.67 x 24.08 ft 76 in stair (dashed) with 0.49 ft spare on the diagonal. +341 SF on this level.
- North stretch strip now ends at x 167 (was 168); drum door on the SW face at (174.8, 249.9), opening into the strip landing, not onto the loop.
- Drum south edge y 248.0: clear of the loop's north edge (y 246) by 2.0 ft; the loop, its R 13 ft NE corner and the upper tiers do not change.

ROOM SCHEDULE — LEVEL 2 (SF net of stairs, inside the envelope)

TAG	ROOM	REV G	REV H	CHANGE
—	Upper tier, fixed (1,100 seats)	6,930	6,930	0
17	Strength & Conditioning	5,038	5,038	0
18	Cross-Training Mat	3,500	3,500	0
19	Men	550	550	0
20	Women	900	900	0
21	Admin	470	470	0
—	L2 Corridor	2,192	2,192	0
—	Upper Concourse (E)	994	994	0
—	Stretch / Warm-up (N)	714	708	-6
—	ST-2 landing / NE corner (not programmed)	141	142	+1
—	Running / training loop	5,006	5,006	0


AREA CHECK (no SF cap, D-056; L1, L2, total vs last rev, D-057)

	REV K / G	REV L / H	CHANGE
L1 footprint (P2-A-101 Rev L)	57,520	57,861	+341
L2 area (envelope - open-to-below)	28,692	29,033	+341
TOTAL GSF	86,212	86,894	+682

L2 = envelope 53,181 SF - open-to-below 24,148 SF (arena 132 x 168 + lobby 58 x 34), the Rev F / G method. Rev K / G baseline = D-079. Carried to P2-G-003 Rev L.

OPEN (not decided here)

- Drum door: 4.6 ft from the door to the loop edge along its swing line; landing at a 76 in stair door needs the architect (IBC 1010 not checked; P2-G-002 Rev E F2).
- Drum floor-to-floor, wall and roof; structure of the curved shell; tier depth 1'-6" or less (D-061).
- SRM / Summertown Metals roles are not agreed; names are descriptive, no marks used (D-042).

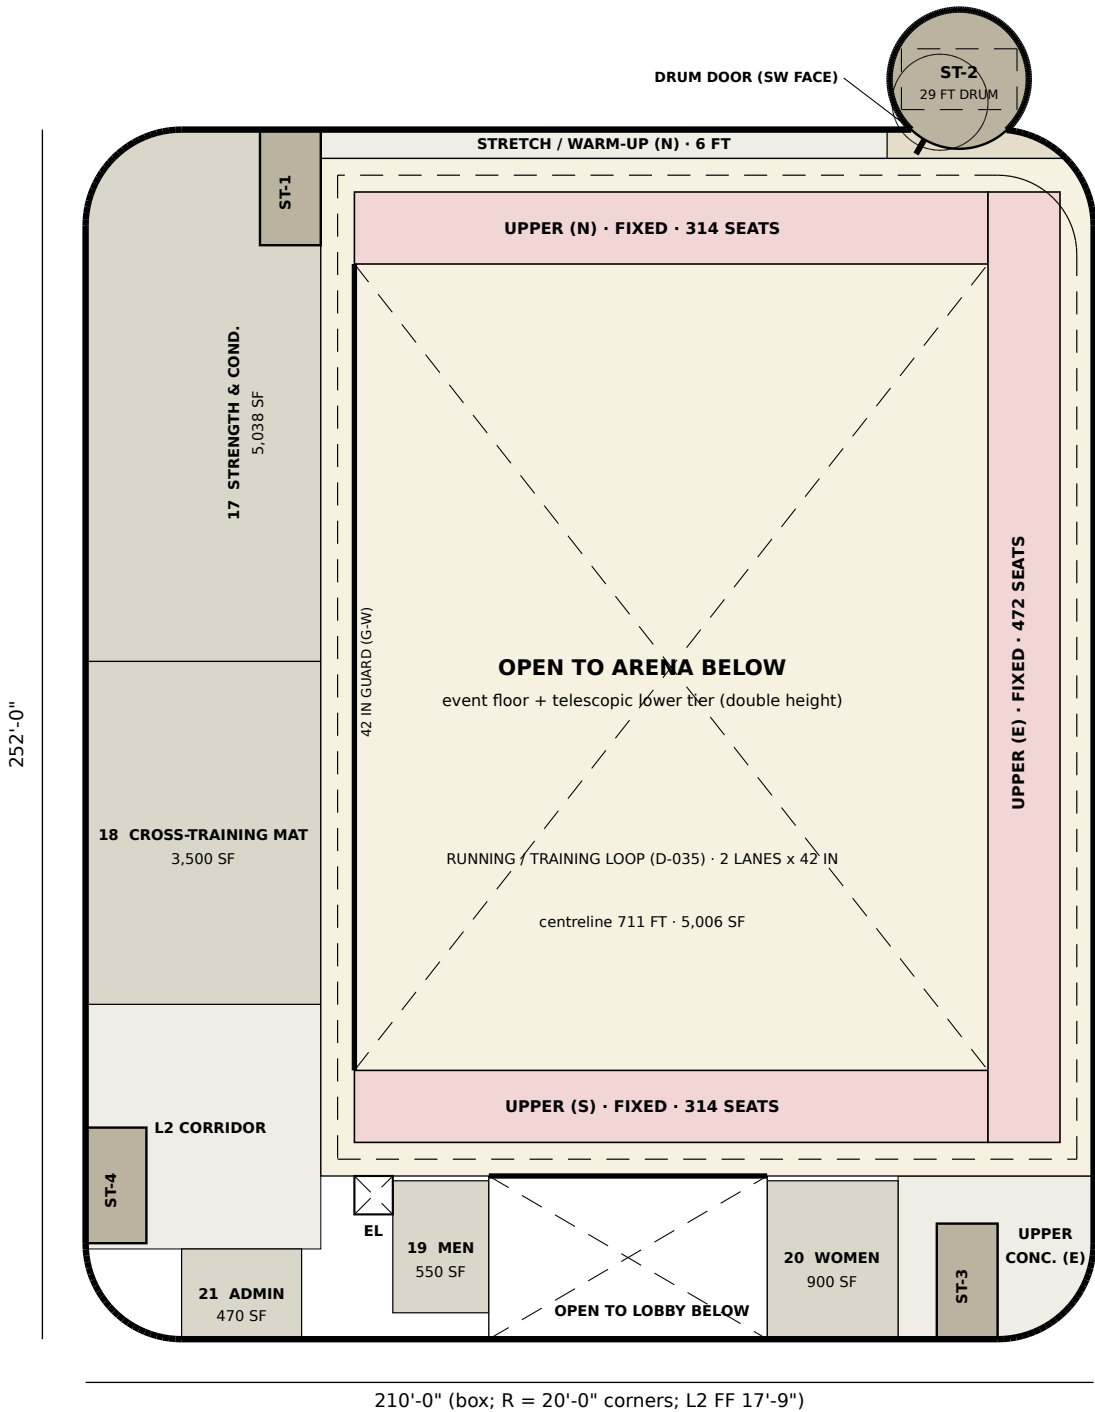

Sources: ARENA P2-A-102_RevG.dxf; params/phase2_plan_rev_i.yaml (L2 as Rev F); phase2_plan_rev_k.yaml; phase2_plan_rev_g_l2.yaml; phase2_plan_rev_l.yaml; D-079..D-081.

PRELIMINARY — CONCEPTUAL DESIGN — NOT FOR CONSTRUCTION

PROJECT Hazel Green Regional Athletic Complex Trojan Horse Arena · Hazel Green area, Madison County, Alabama (site TBD, D-006)	PHASE PHASE 2	SHEET TITLE OVERALL FLOOR PLAN LEVEL 2 · BLOCK PLAN	SCALE 1" = 40'-0"	DATE October 2026	REV H	DRAWN BY Drawn by KEYSTONE (AI) for Shane Brazelton	SHEET P2-A-102
--	-------------------------	---	---------------------------------------	---------------------------------------	-----------------	---	------------------------------