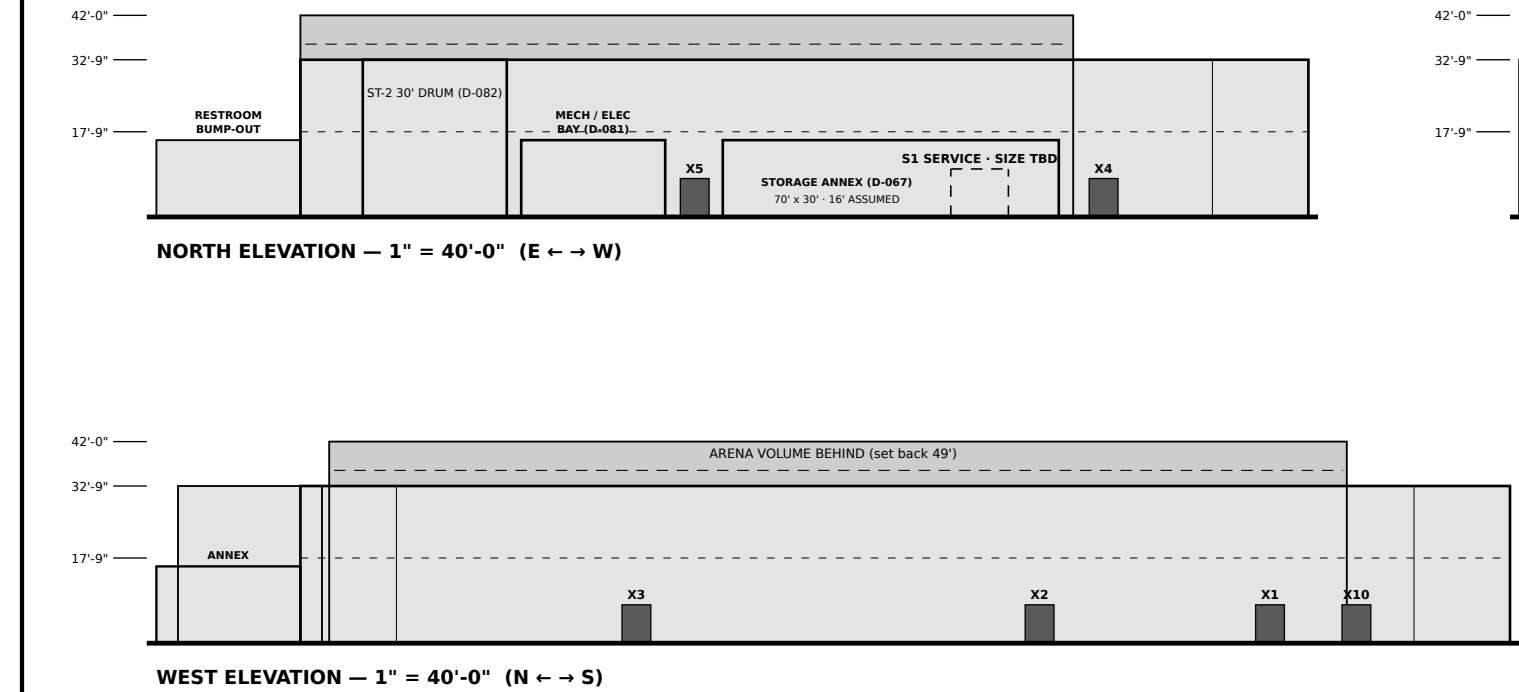
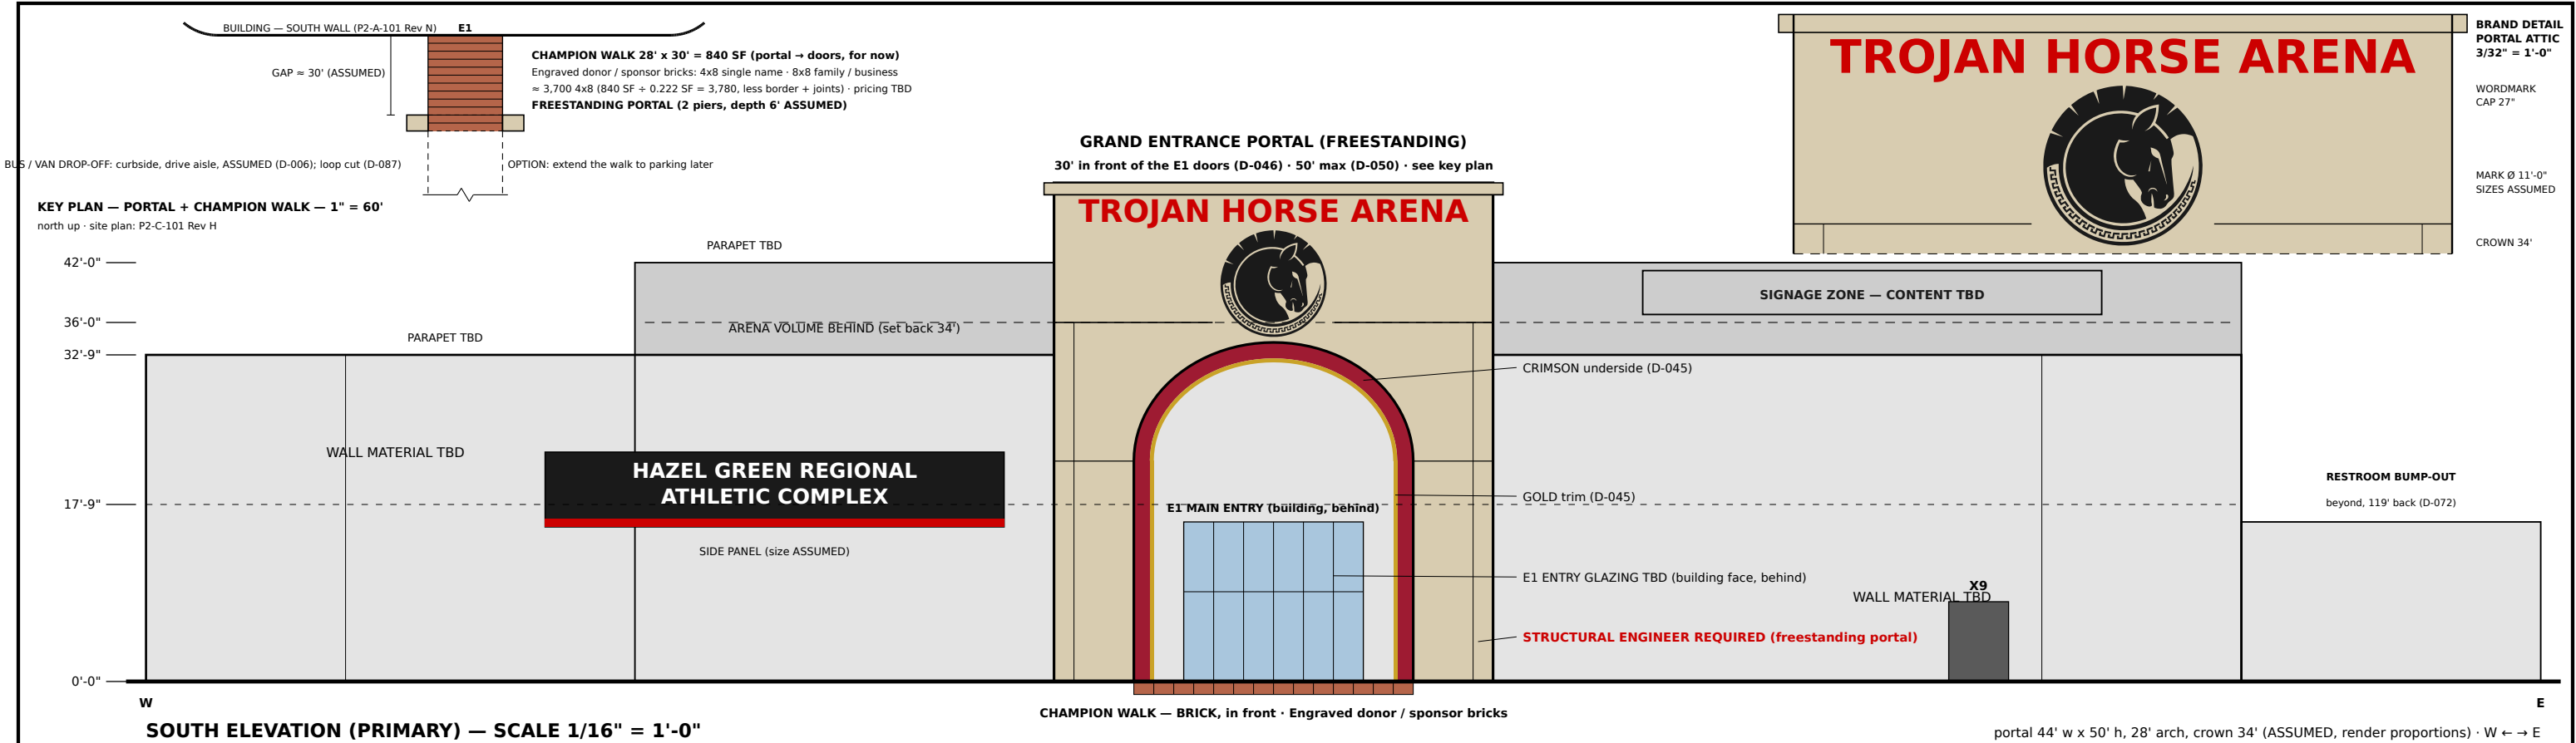


FINISHES

- LIMESTONE (portal) — Shane (material)
- CRIMSON (inside the arch) — Shane (color)
- GOLD (arch soffit) — Shane (color)
- BRAND RED — Shane (red/black brand)
- BRAND BLACK — as brand red
- WALL MATERIAL TBD — TBD
- ARENA VOLUME — WALL / ROOF TBD — TBD
- ENTRY GLAZING (TBD) — TBD
- BRICK (Champion Walk) — Shane (material)

NOTES

- HEIGHTS: L2 FF 17'-9" (D-061 DECIDED), ring roof 32.75' (L2 + 15') ASSUMED. Arena clear ≥ 25' REFERENCE (NFHS via Draper, LA RAP; R-019). U/S structure 36', roof 42' ASSUMED. Upper tier steps DOWN from the loop: 21" risers, front row 9.0' (7'-6" clear, D-061); highest aisle = loop 17.75' (1030.6.2.2 if smoke-protected: ≥ 32.75'; 36' U/S drawn).
- PORTAL: FREESTANDING limestone arch 30' in front of the E1 doors over Champion Walk (D-043, D-046); 50' max (D-050); crown 34', springline 22.1', depth 6' ASSUMED; underside crimson + gold trim (D-045). STRUCTURAL ENGINEER REQUIRED.
- BRAND: official mark Ø 11' (Shane, D-047) at 34.4'-45.4'; wordmark 27" caps, baseline 46.1' (inside the 44' x 50' portal) + side panel, ASSUMED sizes. Trademark search before signage / apparel OPEN (D-042).
- CHAMPION WALK: 28' x 30' brick (for now, D-046); 4x8 single name, 8x8 family / business; ≈ 3,700 4x8; pricing OPEN (D-044); may extend to parking. Bus loop cut (D-087); drop-off curbside (D-006).
- DOORS: symbols (6' x 8' ASSUMED) from P2-A-101 Rev N; X# EXIT ONLY (D-033); X6 on the drum, X7 on the wall, X11 off the corridor, S1 on the annex.
- OUTLINE (P2-A-101 Rev N): R 20' corners (thin lines = tangents), 30' NE drum (D-082), annex 70' x 30', mech / elec bay 30' x 30', bump-out 30' x 56' (16' ASSUMED). Roofs / finishes TBD.
- NOT SHOWN: rooftop units, grading, lighting.
- OPEN QUESTION: ETFE roof / solar (aspirations) — not designed, not in the SF or budget.

PRELIMINARY — CONCEPTUAL DESIGN — NOT FOR CONSTRUCTION

PROJECT	PHASE	SHEET TITLE	SCALE	DATE	REV	DRAWN BY	SHEET
Hazel Green Regional Athletic Complex Trojan Horse Arena · Hazel Green area, Madison County, Alabama (site TBD, D-006)	PHASE 2	EXTERIOR ELEVATIONS SCHEMATIC · COLOR	AS NOTED	October 2026	K	Drawn by KEYSTONE (AI) for Shane Brazelton	P2-A-201