


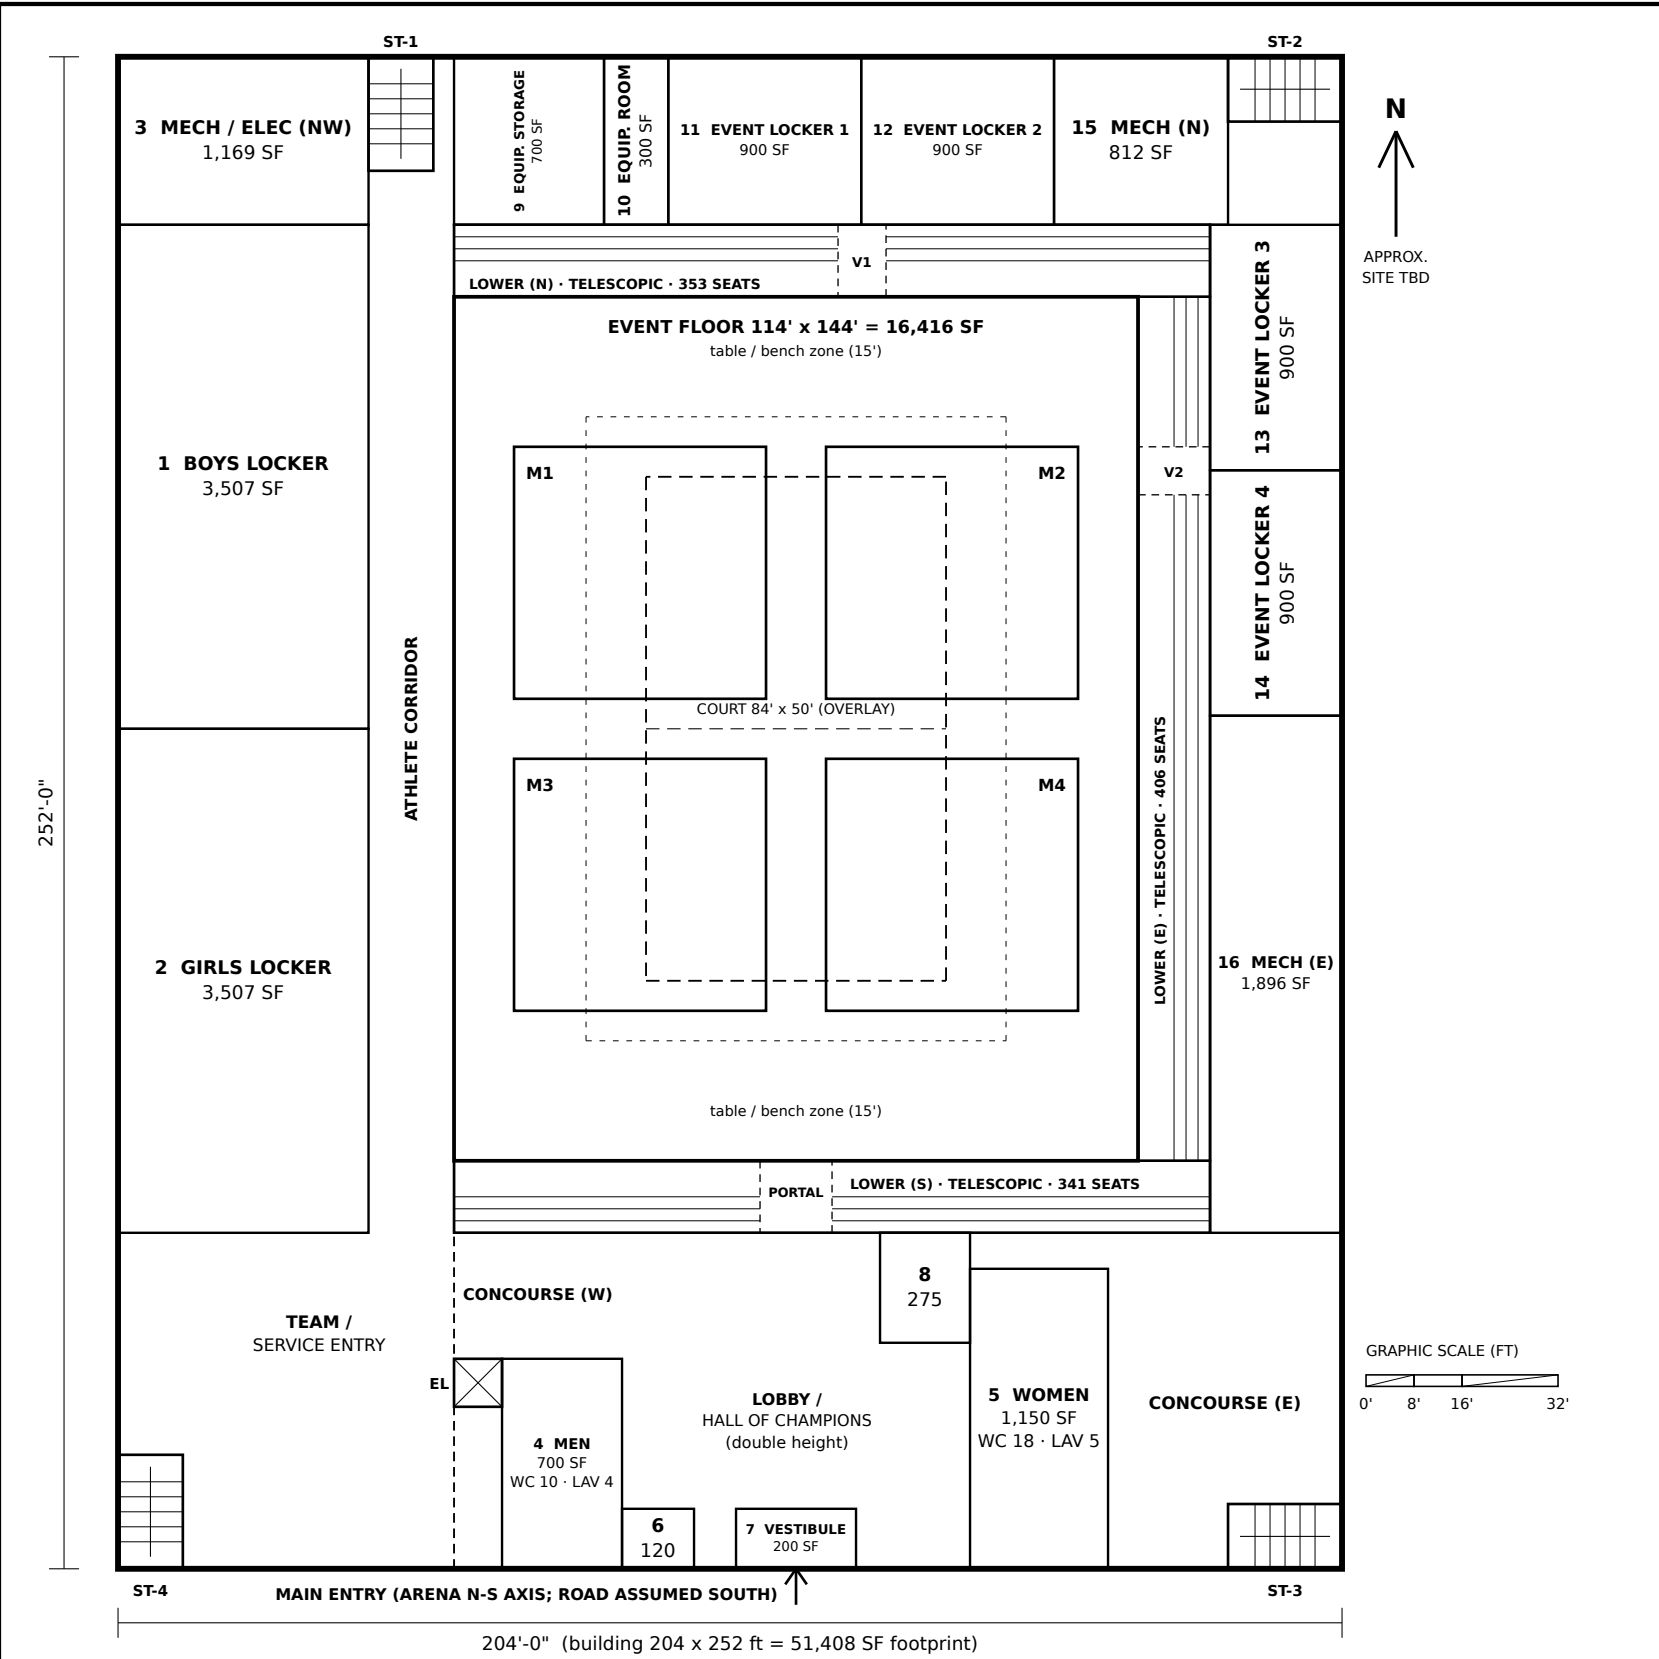

SCHEMATIC — BLOCK PLAN

LEVEL 1 — OVERALL FLOOR PLAN (REV B)

scale 1/32" = 1'-0" on 17 x 11 in · north approximate, road assumed south, site TBD

LEGEND

- Lower tier, TELESCOPIC (extended, 6 rows x 24 in; 3.38 SF/seat) — D-009
- 42' wrestling mat (4, 2 x 2)
- 84' x 50' court + 10' runoff (overlay)
- Portal / vomitory through the telescopic tier (V1, V2)
- Room block (tag number + drawn SF)
- Stair (4) / elevator (X), same position on both levels

ROOM SCHEDULE — LEVEL 1 (drawn vs locked program, P2-G-003 Rev E)

TAG	ROOM	DRAWN SF	PROGRAM	NOTE
—	Event floor (D-030 locked)	16,416	16,400	114' x 144'
—	Lower tier, telescopic (1,100 seats)	4,752	3,719	6 rows; N 353 / S 341 / E 406
1	Boys Locker	3,507	3,500	
2	Girls Locker	3,507	3,503	drawn equal to boys (D-013)
3	Mech / Elec (NW)	1,169	1,162	
4	Men	700	700	14 fixtures (WC 10, LAV 4; urinals ≤ 6 of the WCs)
5	Women	1,150	1,150	23 fixtures (WC 18, LAV 5)
6	First Aid	120	120	
7	Vestibule	200	200	200 of the foyer parts; lobby 400 + desk 200 sit in the lobby
8	Concession	275	275	
9	Equip. Storage	700	700	
10	Equip. Room	300	300	
11	Event Locker 1	900	900	
12	Event Locker 2	900	900	
13	Event Locker 3	900	900	
14	Event Locker 4	900	900	
15	Mech (N)	812	807	
16	Mech (E)	1,896	1,885	

AREA CHECK

Box 204 x 252 ft = 51,408 SF (Rev A 250 x 220): 3,592 SF under the 55,000 cap (target ≥ 2,000). Program footprint 51,130 (P2-G-003 Rev E) fits inside with 278 to spare. Seats: lower 1,100 + upper 1,100 = 2,200 (N 661, S 649, E 890). Mech drawn 3,877 vs 3,854. L1 fixtures 37 flank the lobby; drinking fountains, service sink and 18 wheelchair spaces not drawn.

LAYOUT NOTES (KEYSTONE, ASSUMED — architect to confirm)

- Entry, vestibule, lobby and portal on the arena N-S axis; lobby under the south upper tier, double height to its south.
- Restrooms flank the lobby: men west, women east. Concession in the lobby under the tier; first aid at the entry.
- West side = lockers + athlete corridor only; team / service entry at the SW, gated from the public side (dashed).
- Mech moved to the NW corner, north wall and east ring (behind the bowl). Event lockers N + E via V1/V2.
- Exit separation, travel distance and sightlines NOT checked.

Sources: phase2.yaml (D-009, D-030, D-031); Shane 2026-10-04 4:30 AM CT; P2-G-003 Rev E; R-005, R-008, R-009, R-012, R-014, R-015. Geometry: params/phase2_plan_rev_b.yaml.

PRELIMINARY — CONCEPTUAL DESIGN — NOT FOR CONSTRUCTION

PROJECT	PHASE	SHEET TITLE	SCALE	DATE	REV	DRAWN BY	SHEET
Hazel Green Regional Athletic Complex Trojan Horse Arena · Hazel Green area, Madison County, Alabama (site TBD, D-006)	PHASE 2	OVERALL FLOOR PLAN LEVEL 1 · BLOCK PLAN	1/32" = 1'-0"	October 2026	B	Drawn by KEYSTONE (AI) for Shane Brazelton	P2-A-101