



1 SECTION A-A (NORTH-SOUTH) — looking west

1/32" = 1'-0" · x = 100 (see key plan)

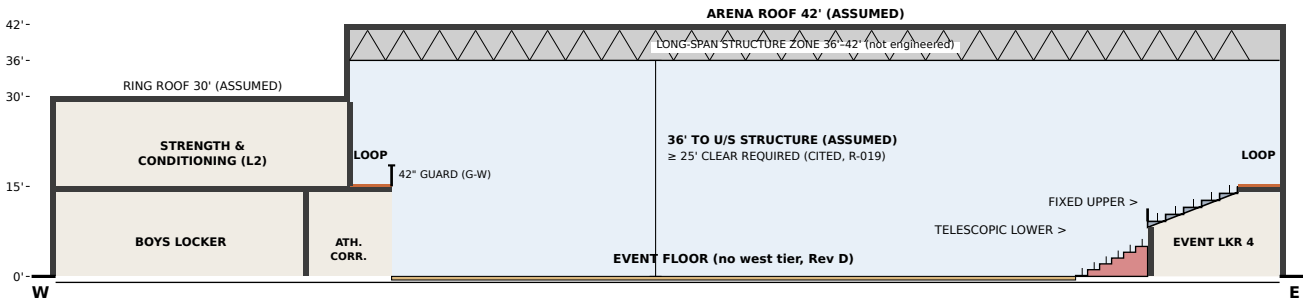


2 SECTION B-B (EAST-WEST) — looking north

1/32" = 1'-0" · y = 150 (see key plan)

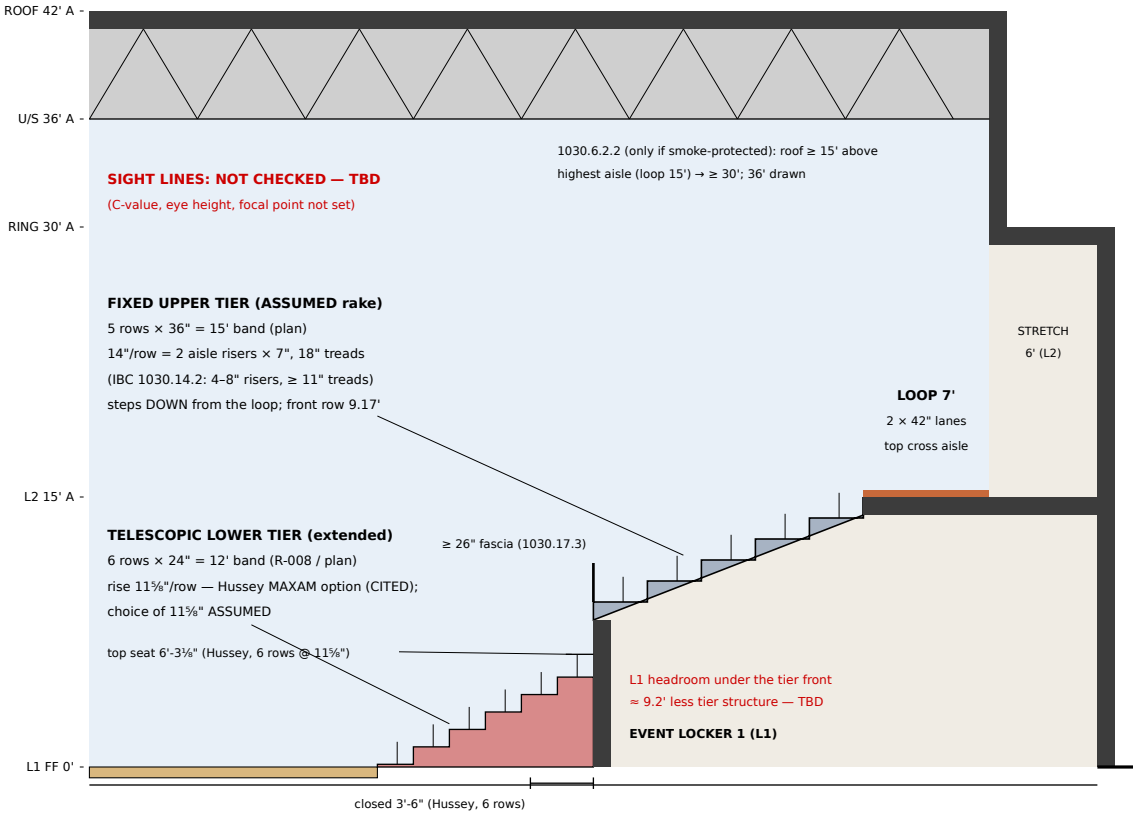


3 NORTH BOWL EDGE (ENLARGED PART OF A-A)

3/32" = 1'-0" · y 196-252 at x = 100

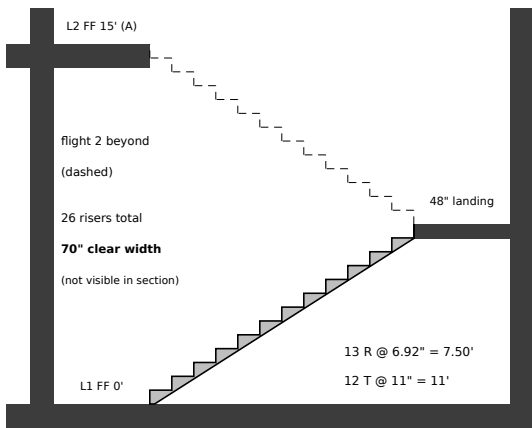


4 TYPICAL EXIT STAIR — 70" CLEAR

1/8" = 1'-0" · D-038 CLOSED

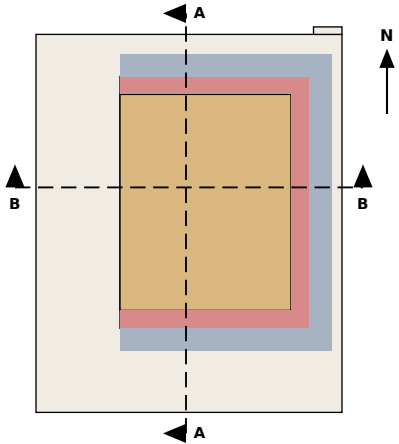

5 KEY PLAN — CUTS

1" = 128' · north up

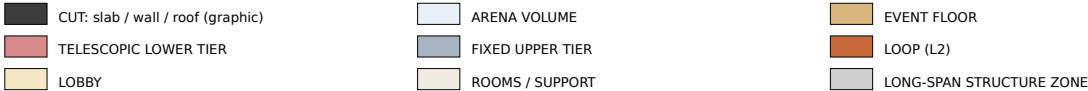

HEIGHTS USED (ft above L1 FF 0'-0")

- L2 FF 15' — ASSUMED (R-015, 15 ft floor-to-floor).
- Ring roof 30' — ASSUMED (L2 + 15 ft).
- Arena structure underside 36' — ASSUMED; ≥ 25' clear over the floor is CITED (R-019: NFHS via Draper, LA RAP) → 11' margin.
- Arena roof top 42' — ASSUMED (36' + 6' long-span structure zone, not engineered).
- Slab, wall and roof thicknesses are graphic only (not designed). Parapets TBD.

SEATING

- Lower tier: telescopic, 6 rows × 24" (R-008, plan Rev D 12' band). Hussey MAXAM rises 9 1/8", 11 1/8", 16" (CITED); 11 1/8" drawn (ASSUMED choice): top seat 6'-3 3/8", closed 3'-6" (Hussey tables). Hussey open depth at 24" is 11'-3" vs the 12' band.
- Upper tier: fixed, 15' band (plan); 5 rows × 36", 14"/row (2 × 7" aisle risers, 18" treads) — ASSUMED, within IBC 2021 1030.14.2. Steps DOWN from the loop (L2 FF = top cross aisle) to a 9.17' front row. Not drawn: tier on the L2 deck rising to ≈ 21' (the 36' basis in phase2\_elev.yaml).
- L1 headroom under the upper-tier front ≈ 9.2' less structure — TBD (architect / structural).
- SIGHT LINES: NOT CHECKED — TBD. Rows and rises are placeholders until a sight-line study (C-value, eye height, focal point).

GUARDS

- Loop open edges G-W (x = 56) and G-S (y = 34): 42" guards, IBC 2021 1015.2 / 1015.3.
- Upper-tier front: sightline-constrained fascia ≥ 26" (1030.17.3); 36" at the foot of aisles (1030.17.4). Type TBD.

STAIRS (ST-1..ST-4)

- 70" clear — D-038 CLOSED (Shane 6:45 AM CT). Handrail projections ≤ 4 1/2" each side (1014.8): architect to confirm how 'clear' is measured.
- 26 risers @ 6.92" (15' ÷ 26), 2 flights of 13, 11" treads, 48" landings (1011.5.2, 1011.6). Stairs are not on cut A-A or B-B; typical shown.
- Plan effect at the next A-101/A-102 revision: ≈ 11.67' × 19' ≈ 221.7 SF per stair per level (+16.5 SF); egress recheck R-018.8. The frozen set stays frozen.

ROOF HEIGHT (IBC 2021 1030.6.2.2)

- Applies only if smoke-protected seating is used: lowest roof deck ≥ 15' above the highest aisle. Highest aisle = the loop at 15' → ≥ 30'; 36' drawn.

CUTS

- A-A: x = 100, looking west (south at left). B-B: y = 150, looking north (west at left). Geometry from P2-A-101/102 Rev D (frozen).
- Colors are graphic only; materials TBD. 'A' = ASSUMED.

PRELIMINARY — CONCEPTUAL DESIGN — NOT FOR CONSTRUCTION

PROJECT

**Hazel Green Regional Athletic Complex**  
**Trojan Horse Arena · Hazel Green area, Madison**  
**County, Alabama (site TBD, D-006)**

PHASE

**PHASE 2**

SHEET TITLE

**BUILDING SECTIONS**  
**SCHEMATIC · COLOR**

SCALE

**AS**  
**NOTED**

DATE

**October**  
**2026**

REV

**A**

DRAWN BY

Drawn by KEYSTONE (AI) for  
Shane Brazelton

SHEET

**P2-A-301**