



EVENT LOCKER ROOM 1 — 900 SF • 18 occ.

1/8" = 1'-0" • door on the E wall → EXIT (N) passage • common path 46 ft ≤ 75 (PASS)

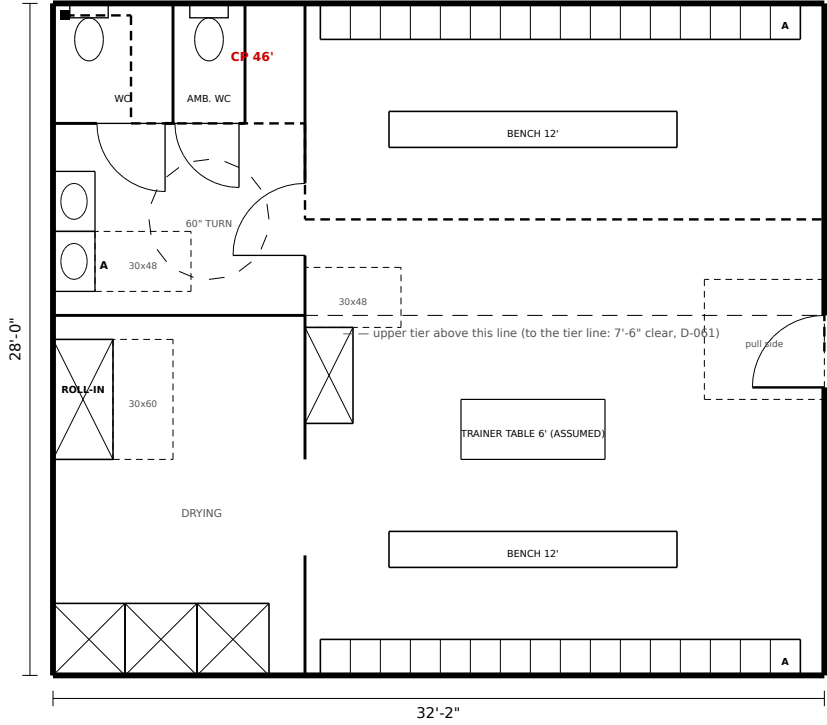


EVENT LOCKER ROOM 2 — 900 SF • 18 occ.

1/8" = 1'-0" • door on the W wall → EXIT (N) passage • common path 46 ft ≤ 75 (PASS)

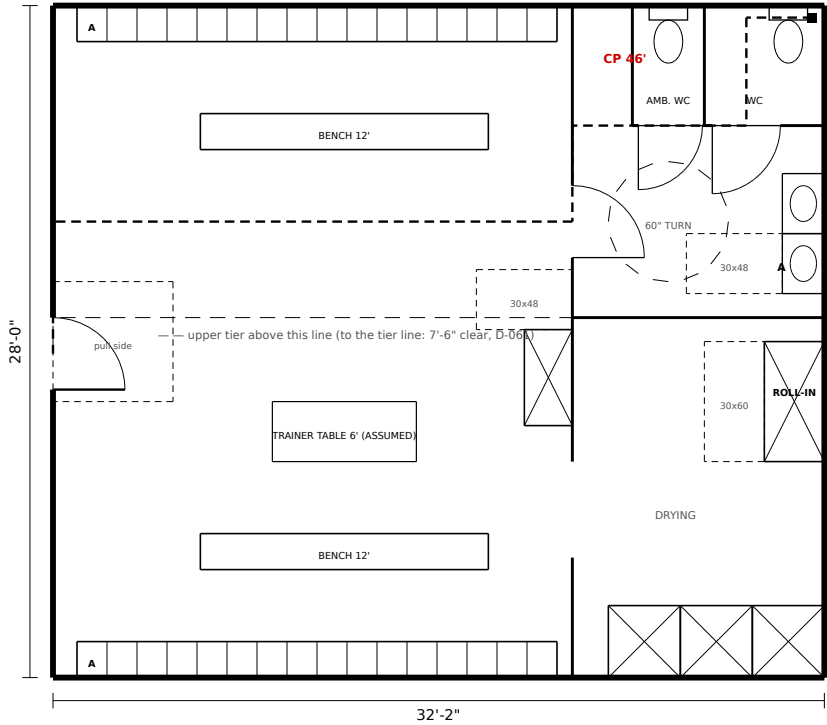


EVENT LOCKER ROOM 3 — 900 SF • 18 occ.

1/8" = 1'-0" • door on the S wall → EXIT (E) passage • common path 51 ft ≤ 75 (PASS)

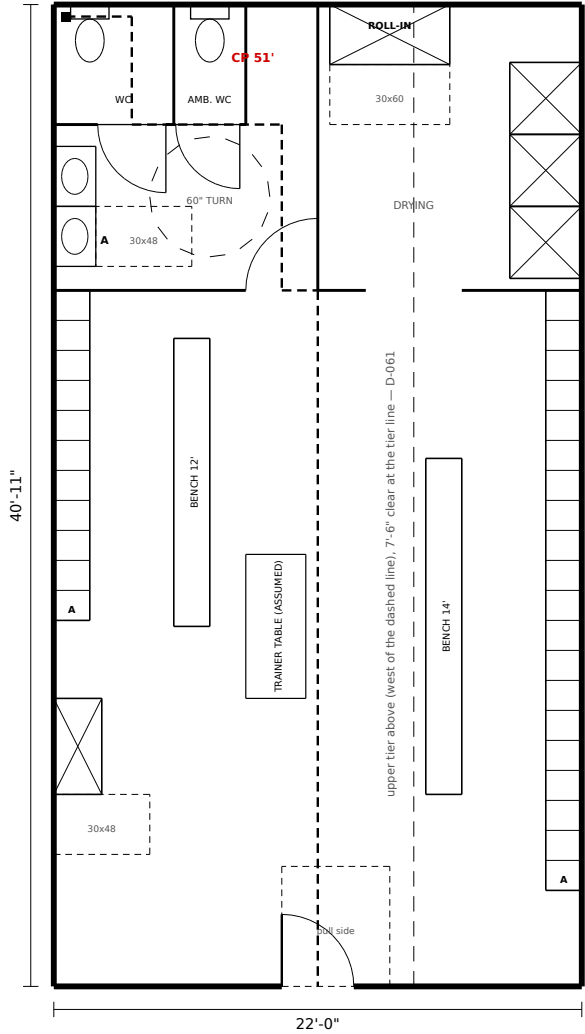


EVENT LOCKER ROOM 4 — 900 SF • 18 occ.

1/8" = 1'-0" • door on the N wall → EXIT (E) passage • common path 51 ft ≤ 75 (PASS)

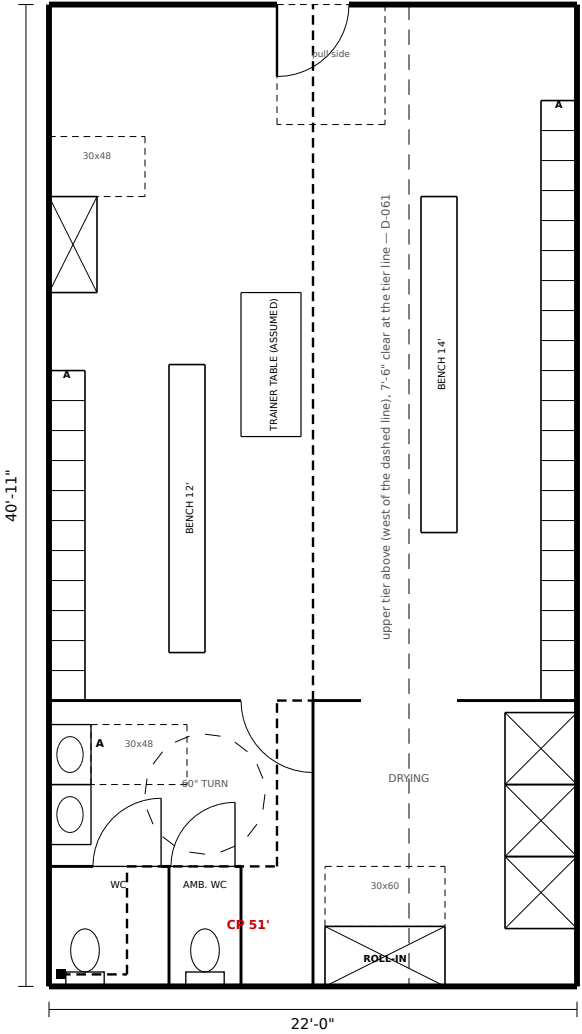

KEY PLAN — L1 (A-101 I)

1" = 250' • grey = rooms 1-4

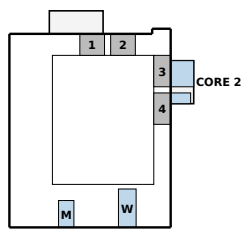

CORE 2 AREA (SF)

Men (2), 26 x 14
Women (2), 30 x 34
DF alcove + janitor, 4 x 14
Corridor = EXIT (E) passage, 30 x 8
BUMP-OUT 30 x 56 (A-101 I)

DRAWN

364
1,020
56
240
1,680

TEST-FIT NET

331.5
924

WALLS / CHASE

+9.8 %
+10.4 %
target +10 %

WHY EAST: East, not north: the north side is the back-of-house yard (service drive, S1 apron, storage annex x 52-122, X4 / X5 / ST-2 discharges); the east side is open, and the public reaches core 2 straight from the floor and the east lower tier through V2 and the 8 ft EXIT (E) passage. East concourse width and SW FLEX unchanged (D-039).

Public toilets within one storey and 500 ft of every seat (IBC 2902.3.3): PASS. Plumbing on the east side (waste / vent): MEP. Floor chair layouts must keep an aisle to V2 (core 2 is reached only through V2 / EXIT (E)).

Sources: params/phase2_enlarged.yaml, phase2_enlarged_rev_c.yaml, phase2_plan_rev_i.yaml, phase2_program.yaml (rev_k); IBC 2021 T2902.1, 2902.1.1, 2902.3.3, 1003.6, 1006.2.1, T1017.2; IPC 2021 405.3.1, 405.3.5, 424.2 (UpCodes, retrieved 2026-10-04); ADA 2010 211.2, 213.3, 304.3, 602, 604.8, 605, 606 (www.ada.gov); D-039, D-064, D-068, D-069; Shane 2026-10-04 3:31 PM CT.

Schematic enlarged plans: fixture counts, benches, lockers and showers ASSUMED (KEYSTONE). Accessible fixture sizes are ADA 2010 minimums for the architect to develop; not a code review (D-008).

COMMON PATH — VERIFIED ON THIS LAYOUT (T1006.2.1)

One exit access doorway allowed when the space holds ≤ 49 occupants and the common path of egress travel is ≤ 75 ft (Group A, sprinklered) — IBC 2021 1006.2.1, Table 1006.2.1.

ROOM	OCC.	WORST POINT	CP ft	RESULT	+ TO EXIT
1	18	accessible WC far corner	45.6	≤ 75 PASS	X5 64 ft
2	18	accessible WC far corner	45.6	≤ 75 PASS	X5 64 ft
3	18	accessible WC far corner	50.9	≤ 75 PASS	X7 96 ft
4	18	accessible WC far corner	50.9	≤ 75 PASS	X7 96 ft

Rooms 1-4 unchanged (Rev A approved, D-068). Rooms 3-4 now reach X7 through the bump-out corridor (+30 ft): travel ≤ 96 ft vs 250 ft (T1017.2). Locker fixtures as Rev A / B (ADA 604.8, 606, 608, 803, 811, 903).

L1 PUBLIC RESTROOMS — CHAIRS-ONLY (D-064 • D-069 DECIDED, OPTION 2)


Shane 3:31 PM CT: second restroom pair in a one-storey bump-out opposite the lobby core. L1 load chairs-only 2,346 + 1,100 = 3,446 (IBC 2021 T2902.1, 50/50 split 2902.1.1). Lobby core = rooms 4 + 5 as drawn; core 2 = the rest.

FIXTURE	REQ.	LOBBY	CORE 2	TOTAL	RESULT
Men WC (incl. urinals)	22	10	5 + 7 ur	22	PASS
Men lavatories	9	4	5	9	PASS
Women WC	42	18	24	42	PASS
Women lavatories	12	5	7	12	PASS
Drinking fountains	4	2	2 (hi-lo)	4	PASS

Urinals: core 2 7 ≤ 8 = 67 % of its 12 (IPC 2021 424.2: "urinals shall not be substituted for more than 67 percent of the required water closets in assembly and educational occupancies", R-009). 1 accessible urinal (ADA 213.3.3, 605); 1 wheelchair + 1 ambulatory compartment per room (213.3.1, 604.8); 1 accessible lav (606); 60 in turning space (304.3); hi-lo fountains (211.2, 602).

RESTROOM CORE 2 — EAST BUMP-OUT (D-069) • ENLARGED PLAN

1/16" = 1'-0" • plan turned: north → right, building wall (x 210) on top · 30 x 56 = 1,680 SF, one storey

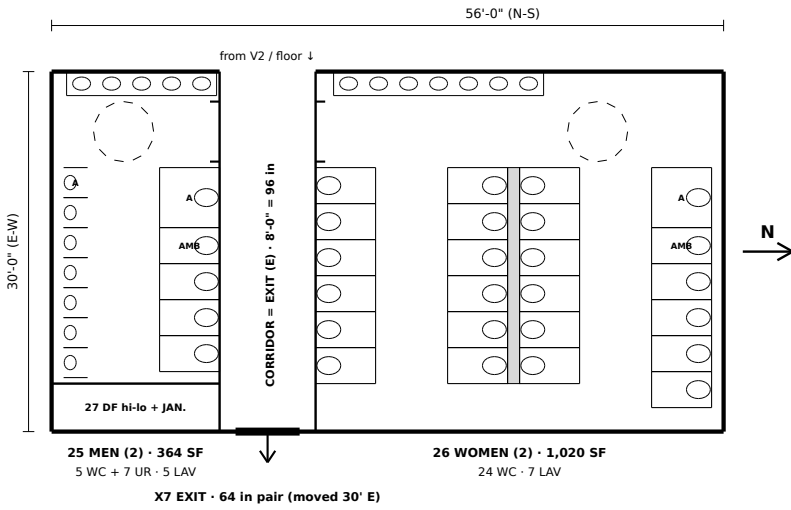

PRELIMINARY — CONCEPTUAL DESIGN — NOT FOR CONSTRUCTION

PROJECT

Hazel Green Regional Athletic Complex
Trojan Horse Arena • Hazel Green area, Madison
County, Alabama (site TBD, D-006)

PHASE

PHASE 2

SHEET TITLE

ENLARGED PLANS
LOCKER RMS + RESTROOM
CORE 2

SCALE

AS
NOTED

DATE

October
2026

REV

C

DRAWN BY

Drawn by KEYSTONE (AI) for
Shane Brazelton

SHEET

P2-A-401