

1 AREA BY LEVEL — 2,200 SEATS, MIX (D-009), L2 LOOP (D-035)

SPACE	REV F LOOP	REV E	BASIS
LEVEL 1 (net SF)			
Event floor (D-030, locked)	16,400	16,400	phase2.yaml · D-030
Lower tier seats (1,100), TELESCOPIC	3,719	3,719	3.38 SF/seat (R-008) · fixed col. 6.0
Boys Locker Room	3,500	3,500	phase2.yaml tag
Girls Locker Room (D-013)	3,503	3,503	phase2.yaml tag; D-013 open
Event / visitor locker rooms	3,600	3,600	4 x (14 wrestlers + 4 staff) x 50 SF
Foyer / trophy lobby (hall of champions)	800	800	200 + 400 + 200 (Loudoun 2014)
Lower concourse	1,375	1,375	25% of seats x 5 SF standing (T1004.5)
Public restrooms L1 (37 fixtures)	1,850	1,850	T2902.1 x 50 SF (R-009)
Concession stand	275	275	Loudoun kitchen proxy; D-011
First aid	120	120	Loudoun 2014; 1 room counted
Equipment storage (mats + floor covers)	700	700	Loudoun gym storage proxy
Equipment room	300	300	Loudoun equip./maint. proxy
Stairs (4) + elevator	874	890	R-015
L1 net	37,016	37,032	
Mechanical (5% of total gross, at grade)	3,939	3,854	R-014 · LOW
L1 GROSS (x 1.25)	51,194	51,108	R-014 gross-up
LEVEL 2 (net SF)			
Upper tier seats (1,100), FIXED	6,600	6,600	6.0 SF/seat (R-008)
Strength & Conditioning	5,224	6,000	D-035: was 6,000 (trimmed for the loop)
Cross-Training Mat Area	3,500	4,000	D-035: was 4,000 (trimmed for the loop)
Administrative office	470	470	150 + 120 + 200 (Loudoun 2014)
Upper concourse / balcony	—	1,375	Rev E only; the loop replaces it
Public restrooms L2 (29 fixtures)	1,450	1,450	T2902.1 x 50 SF (R-009)
Stairs (4) + elevator	874	890	R-015
L2 net rooms (without the loop)	18,118	20,785	
Running / training loop (drawn, not grossed up)	4,942	—	P2-A-102 Rev D · ASSUMED no x1.25
L2 GROSS (x 1.25 rooms + loop)	27,590	25,981	
FIT CHECK			
Arena volume gross (floor + lower tier, double height)	25,149	25,149	
Arena volume + L2 gross	52,738	51,130	L2 sits over the L1 ring
FOOTPRINT = max(L1, arena volume + L2)	52,738	51,130	mix: set by arena volume + L2
MARGIN under the 55,000 SF cap (D-031)	2,262	3,870	target ≥ 2,000 (Shane)
if the loop were grossed up x1.25: footprint / margin	53,974 / 1,026	—	would miss the target
Meets the ≥ 2,000 SF target?	YES	YES	
TOTAL GSF (2 levels)	78,784	77,089	not capped (D-031)

REV F = Rev E (MIX, D-009) with S&C 5,224 and cross-training 3,500 SF (D-035) and the loop in place of the upper concourse. Loads, stairs and fixtures recomputed (stair width 64.0 in). The loop is circulation drawn at full size, so it is added to L2 gross as drawn (ASSUMED). The arena volume + L2 (52,738) sets the footprint.

2 SEATS BY SIDE AND TIER = 2,200 (= REV E)

SIDE	LOWER (TELE.)	UPPER (FIXED)	TOTAL
North	353	308	661
South	341	308	649
East	406	484	890
TOTAL	1,100	1,100	2,200
capacity drawn	1,306	1,125	2,431

No west tier (OK'd). Lower: 6 rows x 24 in = 12 ft extended (R-008), less the 12 ft portal and two 8 ft vomitories. Upper: 15 ft at 6.0 SF/seat. Each tier = 1,100, split by side in proportion to drawn capacity (P2-A-101/102 Rev B). Spare capacity is left for wheelchair spaces and aisles; the upper tier has only 25 spare. Tiers unchanged in Rev D.

3 LEVEL 2 RUNNING / TRAINING LOOP (D-035)

2 lanes x 42 in = 7 ft all around, squared corners. Centerline 148 x 205 ft: 2 x (148 + 205) = 706 ft; 5,280 / 706 = 7.48 laps/mile. Area 4,942 SF. Lanes: UFC 4-740-02N 4.1.7 (42 in, min 3 lanes), Athletic Business (36-42 in; max 12 laps/mile, 8-10 preferred). 2 lanes is ASSUMED: 3 lanes (10.5 ft) does not fit without moving the upper tier. Event days: upper concourse, spectators cross it at the tier entries; non-event days: training. 42 in guards at open edges (IBC 1015.2, 1015.3).

4 FIXTURES BY LEVEL (IBC 2021 T2902.1)

LEVEL	LOAD	WC M	WC W	LAV M	LAV W	DF	SUM
L1	1,428	10	18	4	5	2	37
L2	1,100	8	14	3	4	2	29
TOTAL	2,528	18	32	7	9	4	66

L1 = lower seats + 328 floor occupants (50 SF each); L2 = upper seats. Unchanged from Rev D (load follows seats). Restrooms flank the lobby, L2 stacked over L1.

5 STAIRS, ELEVATOR, WHEELCHAIR

L2 load 1,279 → 4 stairs (T1006.3.3) x 64 in (0.2 in/occ., 1005.3.1), ≈ 203 SF each per level + 1 elevator (1104.4) = 874 SF per level, aligned on both levels. 18 wheelchair spaces + companions (IBC T1109.2.2.1, ADA 221.3), dispersed (ADA 221.2.3) — placement in the telescopic and fixed tiers is an architect task. Rev D moves ST-1, ST-2 and the elevator clear of the loop.

6 RESULT

LOCKED PROGRAM + LOOP
16,400 SF floor · 2,200 seats · 2 levels
L2 loop 706 ft · 7.48 laps/mile
Footprint 52,738 · margin 2,262
Target ≥ 2,000 SF: MET

Total 78,784 GSF (Rev E: 77,089). Drawn building (P2-A-101/102 Rev D) = 204 x 252 ft + 19 x 5 ft NE stair tower = 51,503 SF, 3,497 under the cap. NOTE: the program footprint is 1,235 SF MORE than the drawn building: the drawn plan fits, but the x 1.25 gross-up allowance no longer fully fits inside it.

7 LOCKED IN phase2.yaml

- Event floor 16,400 SF; 4 x 42 ft mats, 2 x 2 (D-030).
- 2,200 seats in the bowl, N, S and E sides; 2 levels; footprint cap 55,000 SF (D-031).
- Seating MIX: telescopic lower tier, fixed upper tier (D-009, Shane 4:30 AM CT).
- S&C 5,224 + cross-training 3,500 SF on Level 2 (D-035; were 6,000 / 4,000).
- Continuous L2 loop, 2 x 42 in (D-035, Shane 4:55 AM CT). Changes only on CHANGE APPROVED.

8 STILL OPEN

- Loop lane count (2 ASSUMED; 3 preferred); 50/50 tier split and 6 telescopic rows (ASSUMED).
- AHJ / code edition (D-008); girls locker size (D-013); concession scope (D-011); owner (D-007); site (D-006).
- Suites PARKED (future add-on).

9 CITED vs ASSUMED


CITED: seat SF and row depth (R-008), fixtures, egress and wheelchair tables (R-009, R-015, R-016), gross-up and mechanical share (R-014), lane width (UFC 4-740-02N, Athletic Business), guards (IBC 1015). ASSUMED: 2 lanes, loop not grossed up, 50/50 tiers, 6 rows, 50 SF/fixture, box shape.


10 SOURCES (retrieved 2026-10-04)

- Shane 2026-10-04 4:55 AM CT (D-035 loop, Rev F); 4:30 AM CT (D-009 mix, margin target)
- R-008, R-009, R-014, R-015, R-016; UFC 4-740-02N; Athletic Business; IBC 2021 1015
- Rev E (mix, no loop) frozen; history in Revs A-E

PRELIMINARY — CONCEPTUAL DESIGN — NOT FOR CONSTRUCTION

PROJECT	PHASE	SHEET TITLE	SCALE	DATE	REV	DRAWN BY	SHEET
Hazel Green Regional Athletic Complex Trojan Horse Arena · Hazel Green area, Madison County, Alabama (site TBD, D-006)	PHASE 2	LOCKED PROGRAM + LOOP D-035 · AREA BY LEVEL ONLY	NTS	October 2026	F	Drawn by KEYSTONE (AI) for Shane Brazelton	P2-G-003

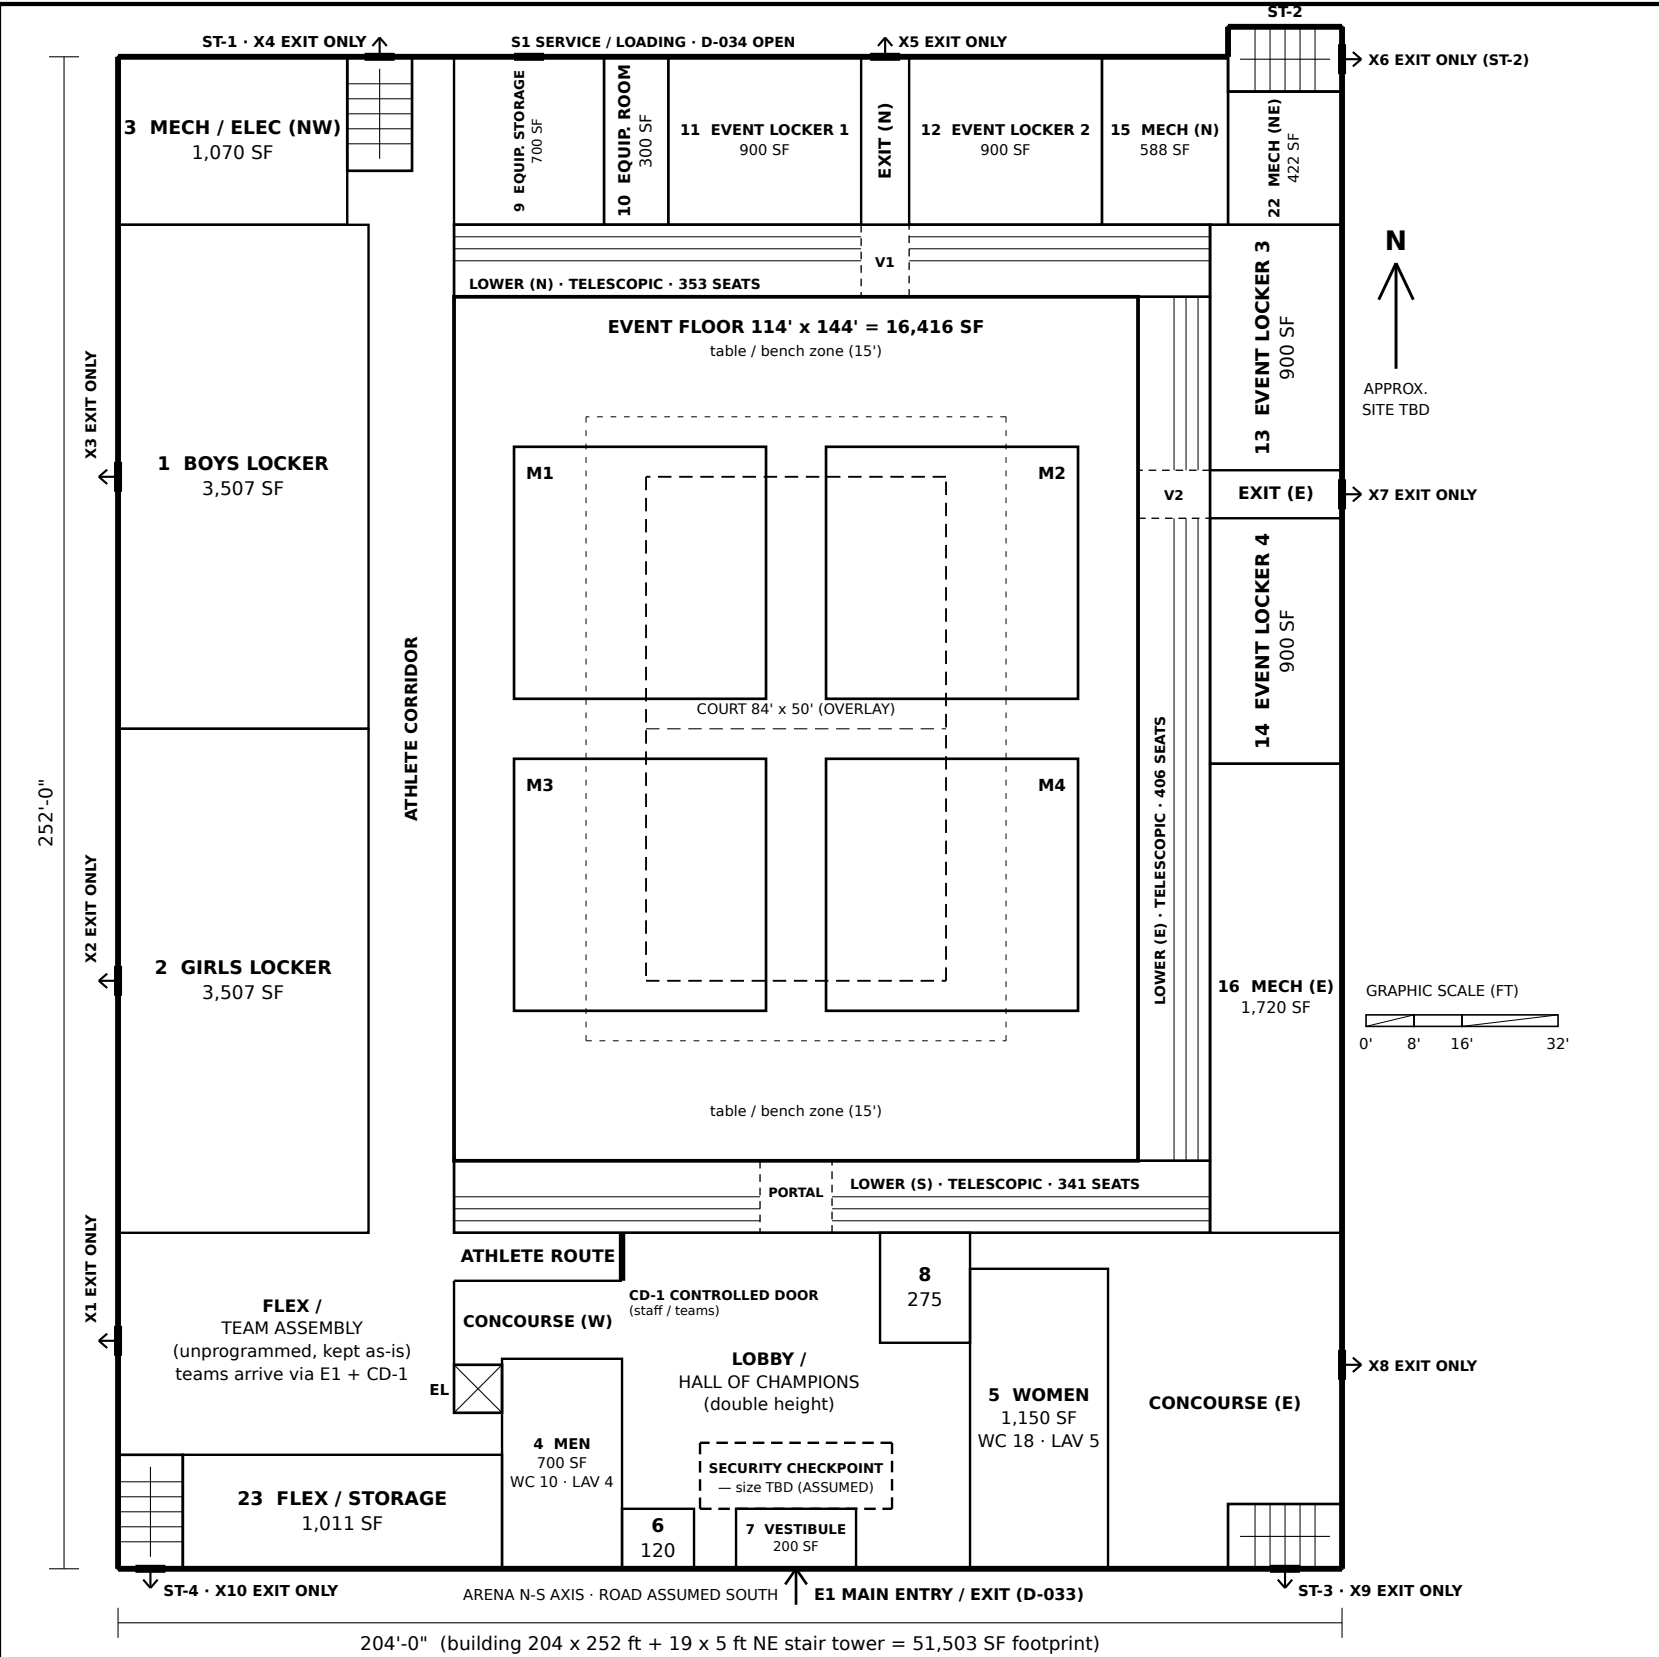

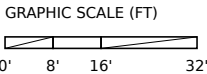

PROJECT	PHASE	SHEET TITLE	SCALE	DATE	REV	DRAWN BY	SHEET
Hazel Green Regional Athletic Complex Trojan Horse Arena · Hazel Green area, Madison County, Alabama (site TBD, D-006)	PHASE 2	OVERALL FLOOR PLAN LEVEL 2 · BLOCK PLAN	1/32" = 1'-0"	October 2026	D	Drawn by KEYSTONE (AI) for Shane Brazelton	P2-A-102