


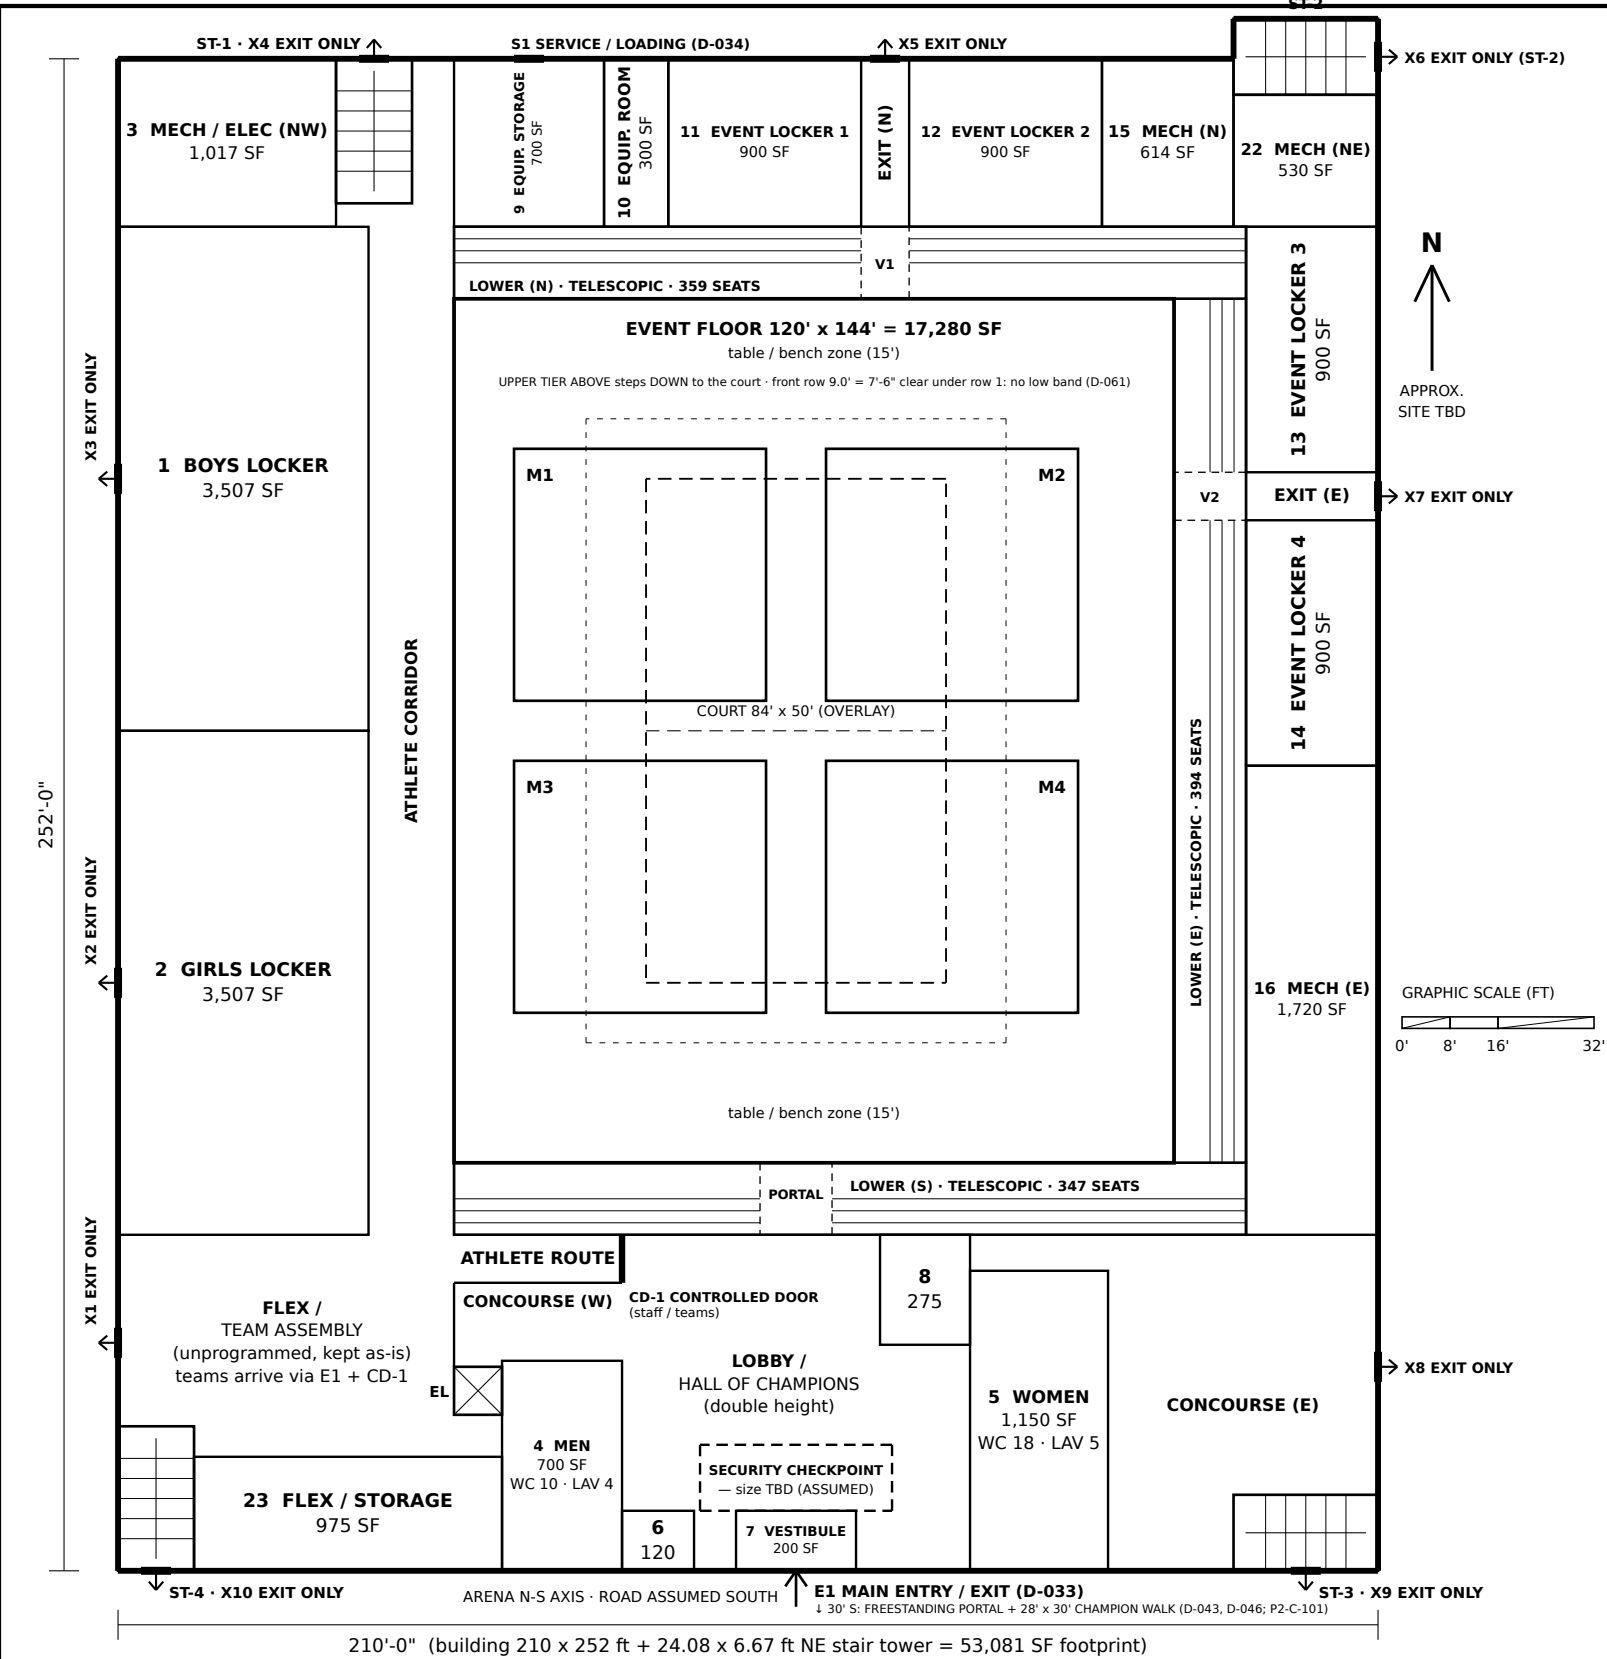

SCHEMATIC — BLOCK PLAN

LEVEL 1 — OVERALL FLOOR PLAN (REV F)

scale 1/32" = 1'-0" on 17 x 11 in · north approximate, road assumed south, site TBD

LEGEND

- Lower tier, TELESCOPIC (extended, 6 rows x 24 in; 3.38 SF/seat) — D-009
- 42' wrestling mat (4, 2 x 2)
- 84' x 50' court + 10' runout (overlay)
- Portal / vomitory through the telescopic tier (V1, V2)
- X# = EXIT ONLY — alarmed, no exterior entry hardware (symbol; width not drawn)
- S1 = SERVICE / LOADING door (staff-controlled, not a people entrance; D-034)
- Upper tier above: front row 9.0' = 7'-6" clear, no low band (D-061)
- Security checkpoint zone (size TBD) · CD-1 controlled door (staff / teams)
- Room block (tag number + drawn SF)
- Stair (4) / elevator (X), same position on both levels

ROOM SCHEDULE — LEVEL 1 (DRAWN vs PROGRAM side by side, P2-G-003 Rev I; C-3)

TAG	ROOM	DRAWN SF	PROGRAM	NOTE
—	Event floor + east zone (D-053)	17,280	17,264	120' x 144'; east tier 16 ft from mats
—	Lower tier, telescopic (1,100 seats)	4,896	3,719	6 rows; N 359 / S 347 / E 394
1	Boys Locker	3,507	3,500	
2	Girls Locker	3,507	3,503	drawn equal to boys (D-013)
3	Mech / Elec (NW)	1,017	1,063	
4	Men	700	700	14 fixtures (WC 10, LAV 4; urinals ≤ 6 of the WCs)
5	Women	1,150	1,150	23 fixtures (WC 18, LAV 5)
6	First Aid	120	120	
7	Vestibule	200	200	200 of the foyer parts; lobby 400 + desk 200 sit in the lobby
8	Concession	275	275	
9	Equip. Storage	700	700	
10	Equip. Room	300	300	
11	Event Locker 1	900	900	to the tier line, full 3,600 (D-060): −0
12	Event Locker 2	900	900	to the tier line, full 3,600 (D-060): −0
13	Event Locker 3	900	900	to the tier line, full 3,600 (D-060): +0
14	Event Locker 4	900	900	to the tier line, full 3,600 (D-060): +0
15	Mech (N)	614	642	
16	Mech (E)	1,720	1,797	
22	Mech (NE)	530	554	NE pocket, up to ST-2 (Rev F: west edge with ST-2, D-061)
23	Flex / Storage	975	—	FLEX, unprogrammed, label kept (D-039, C-1)

AREA CHECK — D-057 (no SF cap, D-056)

	DRAWN REV F	REV E	CHANGE	PROGRAM G-003 I	DRAWN — PROG.
L1 FOOTPRINT	53,081	53,062	+18	54,415	−1,335
L2 AREA	28,933	28,914	+18	28,186	+746
TOTAL GSF	82,013	81,976	+37	82,601	−588

Floor 120 x 144, east tier 16 ft from the mats. Program = footprint / L2 gross (R-021). Seats N 673 / S 661 / E 866 (Rev E 673 / 661 / 866). Mech 3,881 vs 4,056. Event lockers 3,600 SF (D-060). FLEX kept: team assembly ≈ 2,072, FLEX / STORAGE 975 SF.

ACCESS CONTROL + EGRESS (D-033 DECIDED; layout ASSUMED)

- ONE WAY IN (D-033): E1 → security checkpoint (size TBD) → lobby; teams go west through CD-1 to team assembly, athlete corridor, lockers.
- X1-X10 EXIT ONLY: alarmed, no exterior entry hardware, free egress (IBC 2021 1010.2), panic hardware (1010.2.9), no delayed egress in Group A (1010.2.13). > 1,000 per story → 4 exits (T1006.3.3); main exit ≥ 1/2 the load (1030.2); checkpoint must not narrow it (R-015).
- S1 service / deliveries at the north door (D-034 DECIDED); team / bus drop loop south, offset E / W of E1. Freestanding portal 30 ft south of E1 over the 28 x 30 ft brick Champion Walk (D-043, D-046, D-050): outside, drawn on P2-C-101 / P2-A-201.
- D-061 (Option B): Level 2 at 17'-9", 21 in upper risers, front row 9.0 ft: 7'-6" clear under row 1 (≈ 1'-6" structure ASSUMED; IBC 1003.2 minimum, no margin), more behind it. EXIT (N), EXIT (E), SE concourse and the lobby / portal / athlete-route edge are clear; no low band, no seats lost. Travel distance NOT checked.

Sources: phase2.yaml (D-009, D-030, D-033-D-035, D-049, D-051-D-053, D-056, D-057, D-060, D-061); Shane 2026-10-04 9:10 + 10:27 AM CT; P2-G-003 Rev I; R-008, R-009, R-014, R-015, R-020-R-022; IBC 2021 Ch. 10 (UpCodes, Alabama); UFC 4-740-02N (retrieved 2026-10-04). Geometry: params/phase2_plan_rev_f.yaml.

PRELIMINARY — CONCEPTUAL DESIGN — NOT FOR CONSTRUCTION

PROJECT	PHASE	SHEET TITLE	SCALE	DATE	REV	DRAWN BY	SHEET
Hazel Green Regional Athletic Complex Trojan Horse Arena · Hazel Green area, Madison County, Alabama (site TBD, D-006)	PHASE 2	OVERALL FLOOR PLAN LEVEL 1 · BLOCK PLAN	1/32" = 1'-0"	October 2026	F	Drawn by KEYSTONE (AI) for Shane Brazelton	P2-A-101