



PARCEL / PROPERTY LINES, SETBACKS, PARKING, UTILITIES, STORMWATER: TBD (D-006)

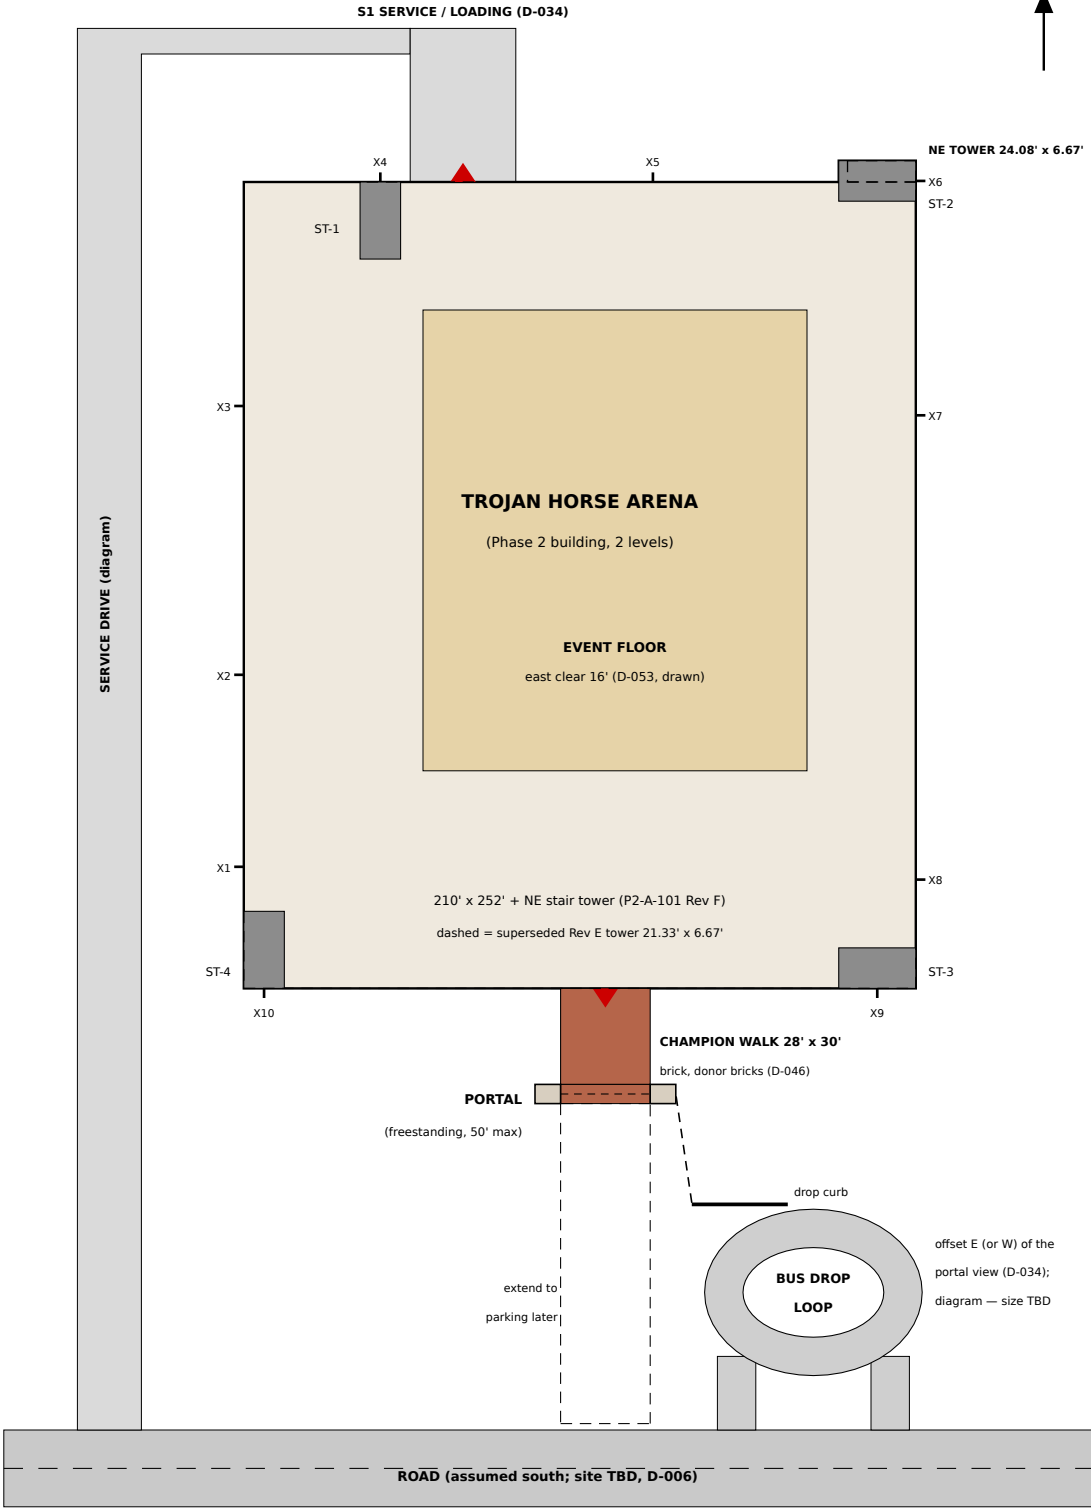

2 ENTRY — PORTAL + CHAMPION WALK — 1" = 30'

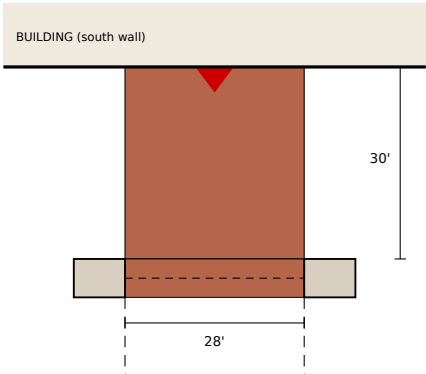

LEGEND

- Building, P2-A-101 Rev F (210' + NE tower)
- Superseded Rev E tower (dashed)
- Exit stairs 76" clear (D-052)
- Event floor
- Champion Walk (brick)
- Portal piers (limestone)
- Service drive / apron (diagram)
- Bus drop loop (diagram)
- Road (assumed)
- E1 main entry / S1 service door

SIZE — D-057 (no cap, no margin; D-056)

|              | DRAWN Rev F | REV E drawn | CHANGE | PROGRAM I | DRAWN — PROG. |
|--------------|-------------|-------------|--------|-----------|---------------|
| L1 FOOTPRINT | 53,080.6    | 53,062.2    | +18.3  | 54,415.1  | −1,334.5      |
| L2 AREA      | 28,932.6    | 28,914.2    | +18.3  | 28,186.3  | +746.3        |
| TOTAL GSF    | 82,013.1    | 81,976.5    | +36.7  | 82,601.4  | −588.2        |

Drawn = P2-A-101/102 Rev F (L2 = L1 minus open-to-below). Program = P2-G-003 Rev I: footprint = the larger of L1 gross and arena volume + L2, plus L2 gross (L1 + L2 gross = 81,119.1). The change is the NE tower growing 2.75' west for the longer ST-2 (L2 17'-9"). Size is set by budget and parcel (D-012, D-006).

STATUS

- SITE TBD (D-006): this is a layout diagram, not a site plan for permit. Parcel, property lines, setbacks, grading, parking count, utilities and stormwater are TBD. AHJ (R-006): Madison County Inspection Department if the parcel is unincorporated (Hazel Green is); the county states no zoning limits on construction; county codes 2018 IBC / IFC / NFPA 101; State Fire Marshal 2021 IFC.

ENTRY (DECIDED)

- Freestanding limestone portal over the walk (D-043), 50' max (D-050), 44' wide x 6' deep (ASSUMED), 30' south of the E1 doors (D-046). Champion Walk 28' x 30' = 840 SF brick, ≈ 3,700 4x8 donor bricks; vendor cost ≈ \$70.9k if all 4x8 (Shane's sheet, D-044 input; install + base not included). Dashed: later extension to parking.

BUS + SERVICE (D-034 DECIDED defaults)

- South bus drop loop offset EAST so it does not block the portal view (west is equally allowed; the SW FLEX / team assembly room would favor west). Drop curb links to the walk's south end. Service / deliveries at the north door S1 by a west-side drive (alignment TBD). Loop, drive and apron are diagrams: lane widths, bus turning template and apron size TBD (civil).

BUILDING (AS DRAWN ON P2-A-101 / A-102 REV F)

- 210' x 252' (unchanged): east seats 16' from the mats (D-053); exits X6-X9 on the east wall. NE stair tower 24.08' x 6.67' = 160.6 SF (Rev E 21.33' x 6.67', dashed). Stairs ST-1..ST-4 76" clear, 12.67' x 24.08', 31 risers (D-052, D-051).
- L2 at 17'-9" with 21" upper risers (D-061 DECIDED, Option B): upper-tier front row 7'-6" clear over the exit paths below; no seats lost. Event lockers 3,600 SF behind the tier (D-060).

FIRE ACCESS / WATER (TBD)

- Fire apparatus access roads, hydrants and fire flow per IFC Appendices B, C, D (State Fire Marshal, 2021 IFC; D107 recommended) and the county's 2018 IFC. Exit discharge from X1-X10 to a public way (IBC 1028) TBD with the parcel.

1 SITE PLAN — CAMPUS DIAGRAM (SITE TBD)

1" = 60'-0" · north approximate · road assumed south · diagram only (no surveyed dimensions)



PRELIMINARY — CONCEPTUAL DESIGN — NOT FOR CONSTRUCTION

|   |         |                                                    |             |                 |     |                                               |          |
|---|---------|----------------------------------------------------|-------------|-----------------|-----|-----------------------------------------------|----------|
| PROJECT   | PHASE   | SHEET TITLE                                        | SCALE       | DATE            | REV | DRAWN BY                                      | SHEET    |
| Hazel Green Regional Athletic Complex<br>Trojan Horse Arena · Hazel Green area, Madison<br>County, Alabama (site TBD, D-006) | PHASE 2 | SITE PLAN — CAMPUS DIAGRAM<br>SITE TBD · SCHEMATIC | AS<br>NOTED | October<br>2026 | C   | Drawn by KEYSTONE (AI) for<br>Shane Brazelton | P2-C-101 |