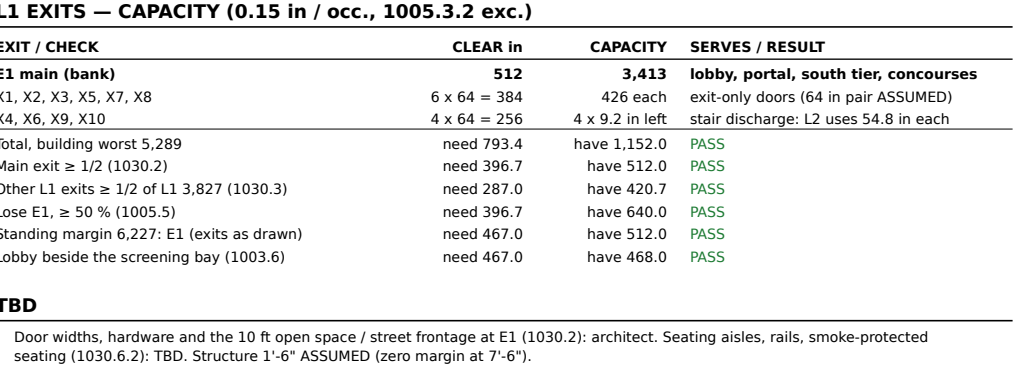


EXIT DISCHARGE — 40 FT WALK (D-066 DECIDED) — CHECK

Exit discharge (1028.3, D-066 DECIDED): walk 40 ft at the doors = 28 ft brick + 2 x 6 ft bands = 480 in $\geq$ 466.5 (standing margin 467.0); at the portal the bands pass outside both 8 ft piers (6 ft each) $\rightarrow$ 28 + 6 + 6 = 40 ft = 480 in; south to the public way 40 ft (site TBD, D-006).

P2-C-101 Rev D.

PRELIMINARY — CONCEPTUAL DESIGN — NOT FOR CONSTRUCTION

PROJECT	PHASE	SHEET TITLE	SCALE	DATE	REV	DRAWN BY	SHEET
Hazel Green Regional Athletic Complex Trojan Horse Arena · Hazel Green area, Madison County, Alabama (site TBD, D-006)	PHASE 2	LIFE SAFETY PLAN LEVELS 1 + 2 · SCHEMATIC	1" = 50'-0"	October 2026	B	Drawn by KEYSTONE (AI) for Shane Brazelton	P2-A-111