


LEVEL 1 — OVERALL FLOOR PLAN

SCHEMATIC — BLOCK PLAN · scale 1/32" = 1'-0" on 17 x 11 in · north approximate, site TBD

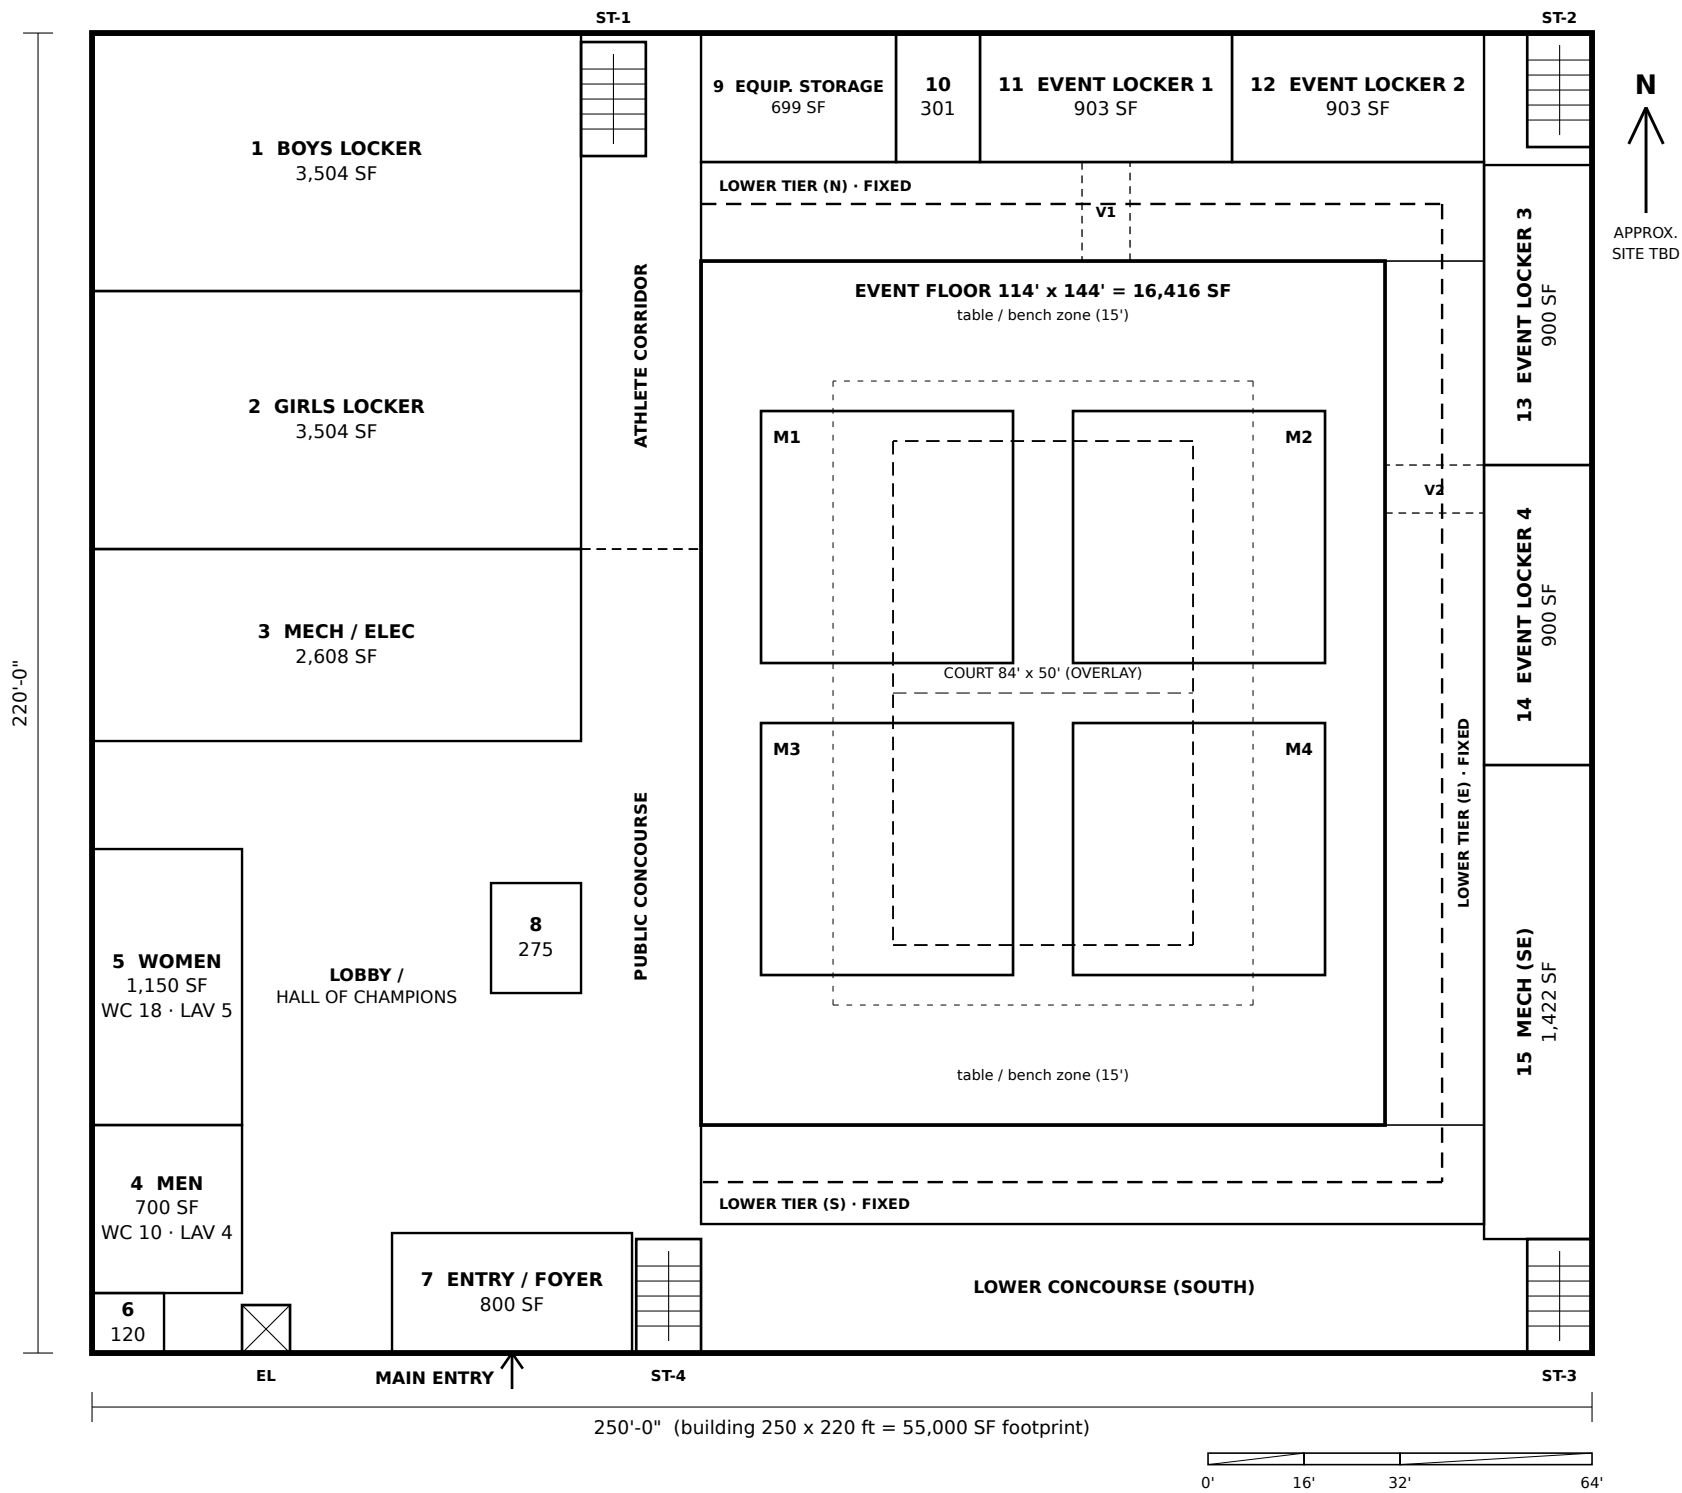

SCHEMATIC — BLOCK PLAN

LEGEND

- Lower tier, FIXED seating (6.0 SF/seat) — base
- TELESCOPIC overlay: tier depth if bleachers (3.38 SF/seat) — D-009 OPEN
- 42' wrestling mat (4, 2 x 2)
- 84' x 50' court + 10' runout (overlay)
- Room block (tag number + drawn SF)
- Stair (4) / elevator (X), aligned on both levels

ROOM SCHEDULE — LEVEL 1 (drawn vs locked program, P2-G-003 Rev D, fixed)

TAG	ROOM	DRAWN SF	PROGRAM	NOTE
—	Event floor (D-030 locked)	16,416	16,400	114' x 144'
—	Lower tier, fixed (~1,100 seats)	6,682	6,600	telescopic line 9.5' deep
1	Boys Locker	3,504	3,500	
2	Girls Locker	3,504	3,503	drawn equal to boys (D-013)
3	Mech / Elec	2,608	2,630	
4	Men	700	700	14 fixtures (WC 10, LAV 4; urinals ≤ 6 of the WCs)
5	Women	1,150	1,150	23 fixtures (WC 18, LAV 5)
6	First Aid	120	120	
7	Entry / Foyer	800	800	
8	Concession	275	275	
9	Equip. Storage	699	700	
10	Equip. Room	301	300	
11	Event Locker 1	903	900	
12	Event Locker 2	903	900	
13	Event Locker 3	900	900	
14	Event Locker 4	900	900	
15	Mech (SE)	1,422	1,416	

AREA CHECK

Drawn footprint 55,000 SF = cap 55,000 (D-031). Program L1 gross 54,949 fixed / 50,868 telescopic (P2-G-003 Rev D): the block uses all of it; space beyond the program is lobby and concourse. Mechanical drawn 4,030 vs 4,047 program. Fixtures: L1 load 1,428 → 37 in two rooms; 2 drinking fountains + 1 service sink in concourse alcoves (not drawn). 18 wheelchair spaces + companions across both tiers (not drawn).

LAYOUT NOTES (KEYSTONE, ASSUMED — architect to confirm)

- Lockers west next to the floor via the athlete corridor, kept off the public concourse (DR1). Girls drawn equal to boys (D-013).
- Entry + foyer at the south end of the west wing (reference plan: south-center); concourse spine runs north along the floor.
- Event lockers split north (1-2) and east (3-4); vomitories V1/V2 through the tier are TBD. No tier on the west; stage TBD (no source).
- Table/bench zones 15 ft N and S; court overlay long axis N-S. Exit separation, travel distance and sightlines NOT checked.

Sources: phase2.yaml (locked, D-030, D-031); P2-G-003 Rev D; R-005, R-008, R-009, R-012, R-014, R-015; reference plan (Shane). Geometry: params/phase2_plan.yaml.

PRELIMINARY — CONCEPTUAL DESIGN — NOT FOR CONSTRUCTION

PROJECT	PHASE	SHEET TITLE	SCALE	DATE	REV	DRAWN BY	SHEET
Hazel Green Regional Athletic Complex Trojan Horse Arena · Hazel Green area, Madison County, Alabama (site TBD, D-006)	PHASE 2	OVERALL FLOOR PLAN LEVEL 1 · BLOCK PLAN	1/32" = 1'-0"	October 2026	A	Drawn by KEYSTONE (AI) for Shane Brazelton	P2-A-101