


LEVEL 2 — OVERALL FLOOR PLAN

SCHEMATIC — BLOCK PLAN · scale 1/32" = 1'-0" on 17 x 11 in · north approximate, site TBD

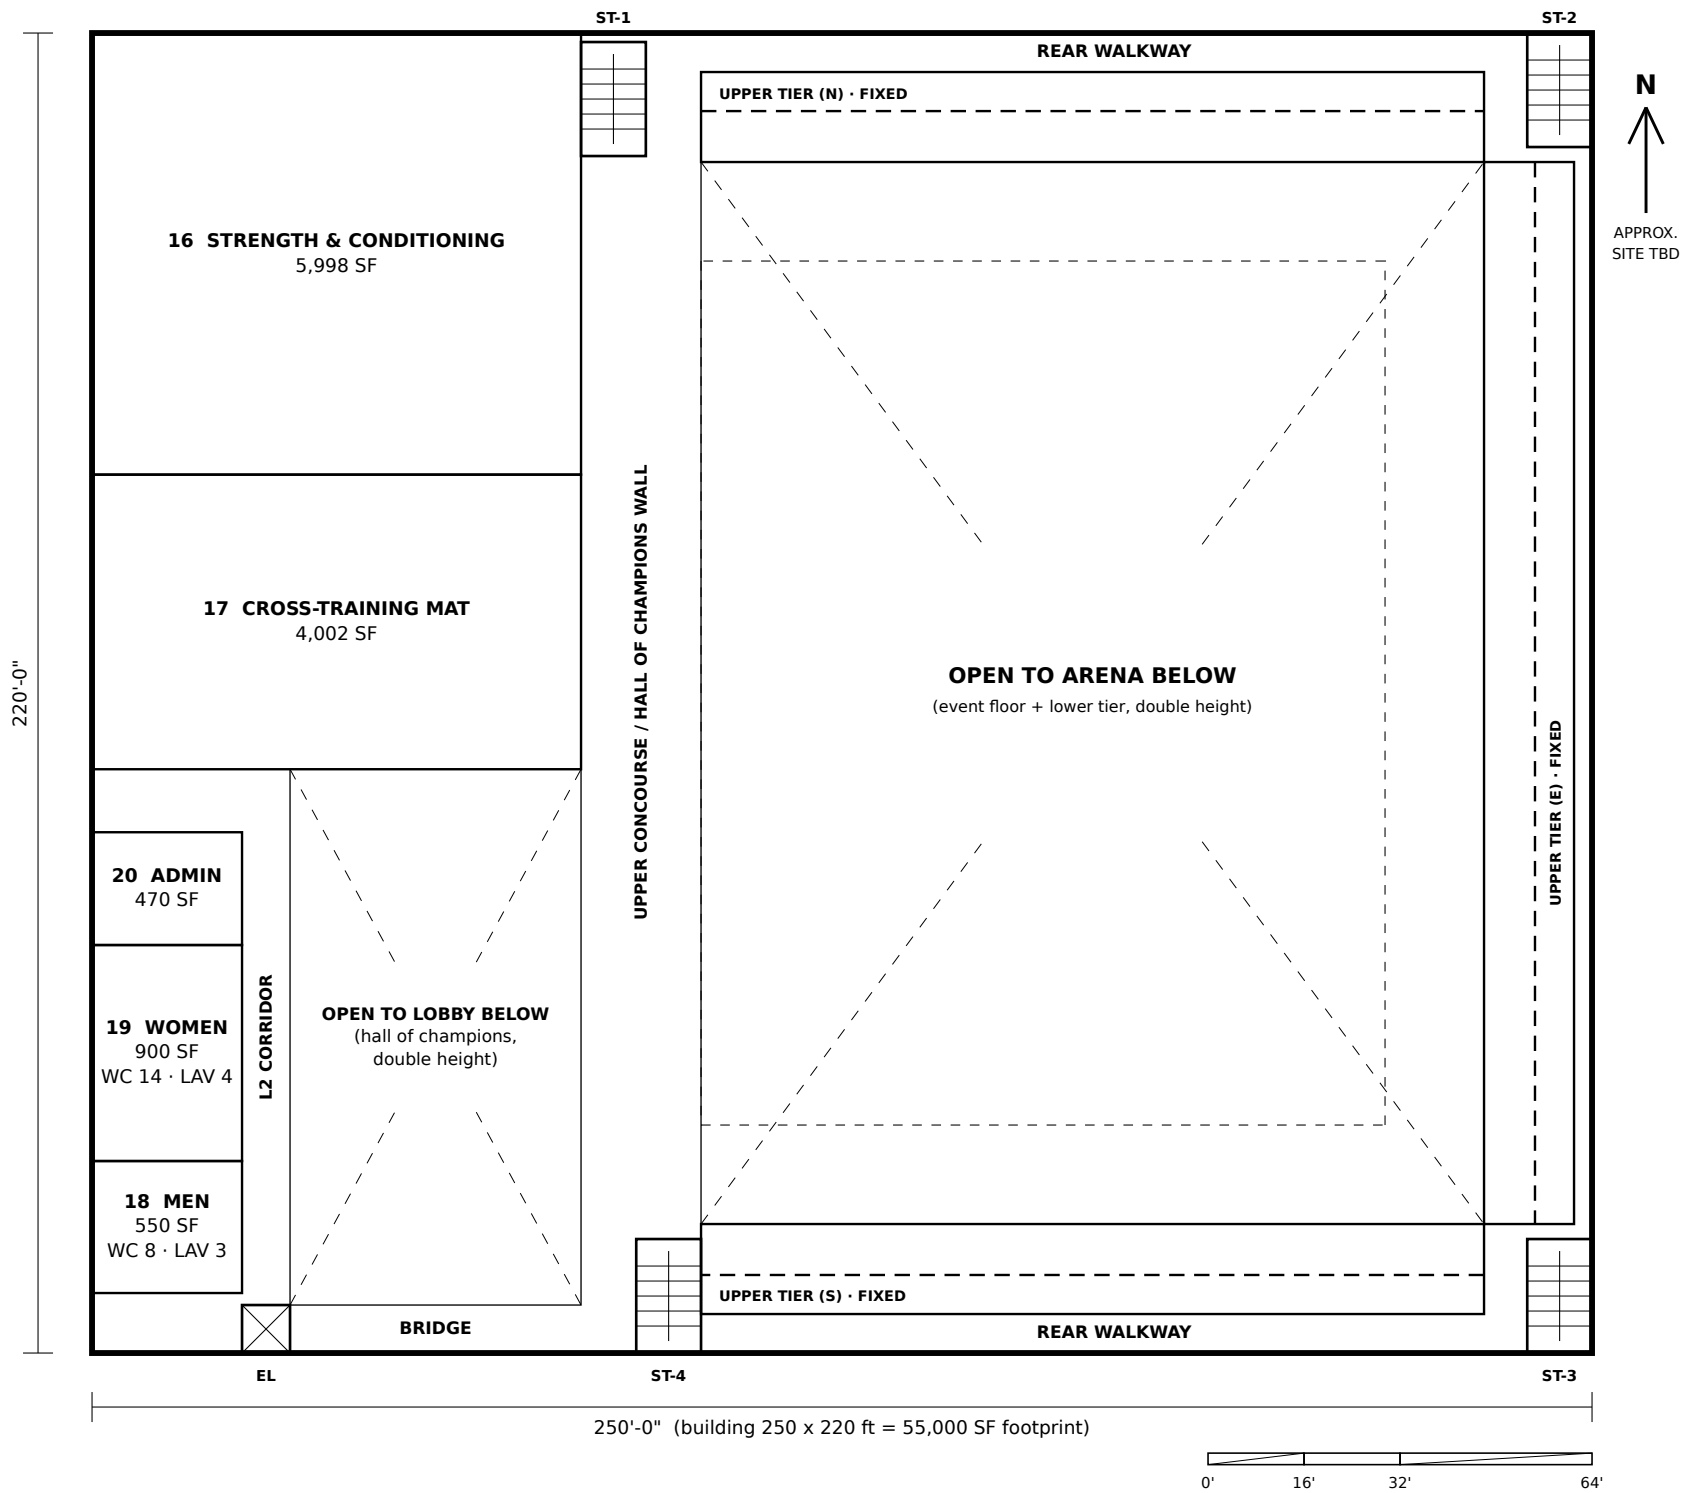

SCHEMATIC — BLOCK PLAN

LEGEND

- Upper tier, FIXED seating (6.0 SF/seat) — base
- TELESCOPIC overlay: tier depth if bleachers (3.38 SF/seat) — D-009 OPEN
- Open to below
- Room block (tag number + drawn SF)
- Stair (4) / elevator (X), aligned on both levels

ROOM SCHEDULE — LEVEL 2 (drawn vs locked program, P2-G-003 Rev D, fixed)

TAG	ROOM	DRAWN SF	PROGRAM	NOTE
—	Upper tier, fixed (~1,100 seats)	6,570	6,600	telescopic line 8.5' deep
16	Strength & Conditioning	5,998	6,000	Level 2 over the lockers (D-030)
17	Cross-Training Mat Area	4,002	4,000	Level 2 over girls locker + mech (D-030)
18	Men	550	550	11 fixtures (WC 8, LAV 3; urinals ≤ 5 of the WCs)
19	Women	900	900	18 fixtures (WC 14, LAV 4)
20	Admin	470	470	

AREA CHECK

Drawn L2 floor 27,570 SF (footprint minus open-to-below) vs program L2 gross 25,981 fixed / 22,380 telescopic; the extra is rear walkways and the upper concourse. Total drawn ≈ 82,570 vs 80,930 program GSF. L2 sits over the L1 ring, nothing over the arena volume. Fixtures: L2 load 1,100 → 29, stacked over L1 rooms. Stair widths: 65 in (R-015).

LAYOUT NOTES (KEYSTONE, ASSUMED — architect to confirm)

- S&C + cross-training on Level 2 over the lockers (D-030); gym floor loads → structural engineer.
- Restrooms + admin stacked over L1 restrooms; L2 corridor + bridge connect the stairs, elevator and upper concourse.
- Upper tier 15 ft deep on N, S and E over the L1 ring; rear walkways N and S. Suites PARKED (none drawn).
- Exit separation, travel distance, sightlines and structure NOT checked. Floor-to-floor 15 ft ASSUMED.

Sources: phase2.yaml (locked, D-030, D-031); P2-G-003 Rev D; R-005, R-008, R-009, R-012, R-014, R-015; reference plan (Shane). Geometry: params/phase2_plan.yaml.

PRELIMINARY — CONCEPTUAL DESIGN — NOT FOR CONSTRUCTION

PROJECT	PHASE	SHEET TITLE	SCALE	DATE	REV	DRAWN BY	SHEET
Hazel Green Regional Athletic Complex Trojan Horse Arena · Hazel Green area, Madison County, Alabama (site TBD, D-006)	PHASE 2	OVERALL FLOOR PLAN LEVEL 2 · BLOCK PLAN	1/32" = 1'-0"	October 2026	A	Drawn by KEYSTONE (AI) for Shane Brazelton	P2-A-102