

SCHEMATIC — BLOCK PLAN

LEVEL 1 — OVERALL FLOOR PLAN (REV J)

scale 1" = 40'-0" on 17 x 11 in · north approximate, road assumed south, site TBD

LEGEND

- Lower tier, TELESCOPIC (extended, 6 rows x 24 in; 3.38 SF/seat) — D-009
- 42' wrestling mat (4, 2 x 2)
- 84' x 50' court + 10' runout (overlay)
- Portal / vomitory through the telescopic tier (V1, V2)
- X# = EXIT ONLY — alarmed, no exterior entry hardware (symbol; width not drawn)
- S1 = SERVICE / LOADING door (staff-controlled, not a people entrance; D-034)
- Upper tier above: front row 9.0' = 7'-6" clear, no low band (D-061)
- Security screening bay, 3 lanes ASSUMED (D-065 Option 1) · CD-1 controlled door
- Room block (tag number + drawn SF)
- Stair (4) / elevator (X), same position on both levels

ROOM SCHEDULE — LEVEL 1 (DRAWN vs PROGRAM side by side, P2-G-003 Rev K; C-3)

TAG	ROOM	DRAWN SF	PROGRAM	NOTE
—	Event floor + east zone (D-053)	17,280	17,264	120' x 144'; east tier 16 ft from mats
—	Lower tier, telescopic (1,100 seats)	4,896	3,719	6 rows; N 359 / S 347 / E 394
1	Boys Locker	3,507	3,500	
2	Girls Locker	3,507	3,503	drawn equal to boys (D-013)
3	Mech / Elec (NW)	1,017	1,180	
4	Men	700	700	lobby core: 14 fixtures (D-069 split)
5	Women	1,150	1,150	lobby core: 23 fixtures (D-069 split)
6	First Aid	120	120	Rev H: moved off the lobby's east side for the screening bay (D-065); east...
7	Vestibule	520	200	Rev G: widened to the 52 ft E1 bank (outer + inner bank, 8 pairs each, AS...
8	Concession	275	275	Rev H: moved off the lobby's east side for the screening bay (D-065) into t...
9	Equip. Storage	700	700	
10	Equip. Room	300	300	
11	Event Locker 1	900	900	to the tier line, full 3,600 (D-060): -0
12	Event Locker 2	900	900	to the tier line, full 3,600 (D-060): -0
13	Event Locker 3	900	900	to the tier line, full 3,600 (D-060): +0
14	Event Locker 4	900	900	to the tier line, full 3,600 (D-060): +0
15	Mech (N)	614	712	
16	Mech (E)	675	783	Rev J: was 1,720 SF (D-072, MEP OPEN)
22	Mech (NE)	530	615	NE pocket, up to ST-2 (Rev F: west edge with ST-2, D-061)
24	Chair / Table / Stage Storage	2,100	2,100	Rev H NEW (D-067): 2,100 SF one-storey annex; 56 chair / table trucks +...
23	Flex / Storage	975	—	FLEX, unprogrammed, label kept (D-039, C-1)
25	Men (2)	364	—	core 2: 5 WC + 7 urinals, 5 lav (D-069)
26	Women (2)	1,020	—	core 2: 24 WC, 7 lav (D-069)
27	Df / Jan.	56	—	core 2: 2 DF (hi-lo) + janitor sink (D-069)
28	Mech (E2)	660	766	in the bump-out (D-072, MEP OPEN)

AREA CHECK — D-057 (no SF cap, D-056)


	DRAWN REV J	REV I	CHANGE	PROGRAM G-003 K	DRAWN - PROG.
L1 FOOTPRINT	56,861	56,861	±0	58,195	-1,335
L2 AREA	28,933	28,933	±0	28,186	+746
TOTAL GSF	85,793	85,793	±0	86,381	-588

Floor 120 x 144, east tier 16 ft from the mats. Program = footprint / L2 gross (R-021). Seats N 673 / S 661 / E 866 (Rev F 673 / 661 / 866). Mech 3,496 vs 4,056. Event lockers 3,600 SF (D-060). FLEX kept: team assembly ≈ 2,072, FLEX / STORAGE 975 SF.

ACCESS CONTROL + EGRESS (D-033 DECIDED; layout ASSUMED)

- ONE WAY IN (D-033): E1 → vestibule → SCREENING BAY, lobby east side (D-065 Option 1; 3 lanes ASSUMED) → lobby. 39 ft = 468 in clear beside the bay ≥ 466.5 in standing (IBC 1003.6, 1010.5). First aid + concession in the E concourse.
- CORE 2 (D-069 / D-070 / D-072): 30 x 56 bump-out slid 42 ft south of EXIT (E). PUBLIC CORRIDOR (E) 8 ft from CONCOURSE (E): rooms 25 / 26 / 27 open only onto it; X11 off it. EXIT (E) clear, X7 on the wall. MECH (E) 675 + (E2) 660 SF (MEP OPEN). Fixtures 22 / 42 WC with the lobby core. Checks: A-111 D, A-401 D.
- D-061 (Option B): Level 2 at 17'-9", 21 in upper risers, front row 9.0 ft: 7'-6" clear under row 1 (≈ 1'-6" structure ASSUMED; IBC 1003.2 minimum, no margin). Exit paths under the tier are clear; no low band, no seats lost.

Sources: phase2.yaml (D-033-D-069); DECISIONS_ARENA D-070-D-072; P2-G-003 K, A-111 D, A-401 D; IBC 2021 1003.6, 1006.2.1, 1020.3, T2902.1. Geometry: params/phase2_plan_rev_j.yaml.

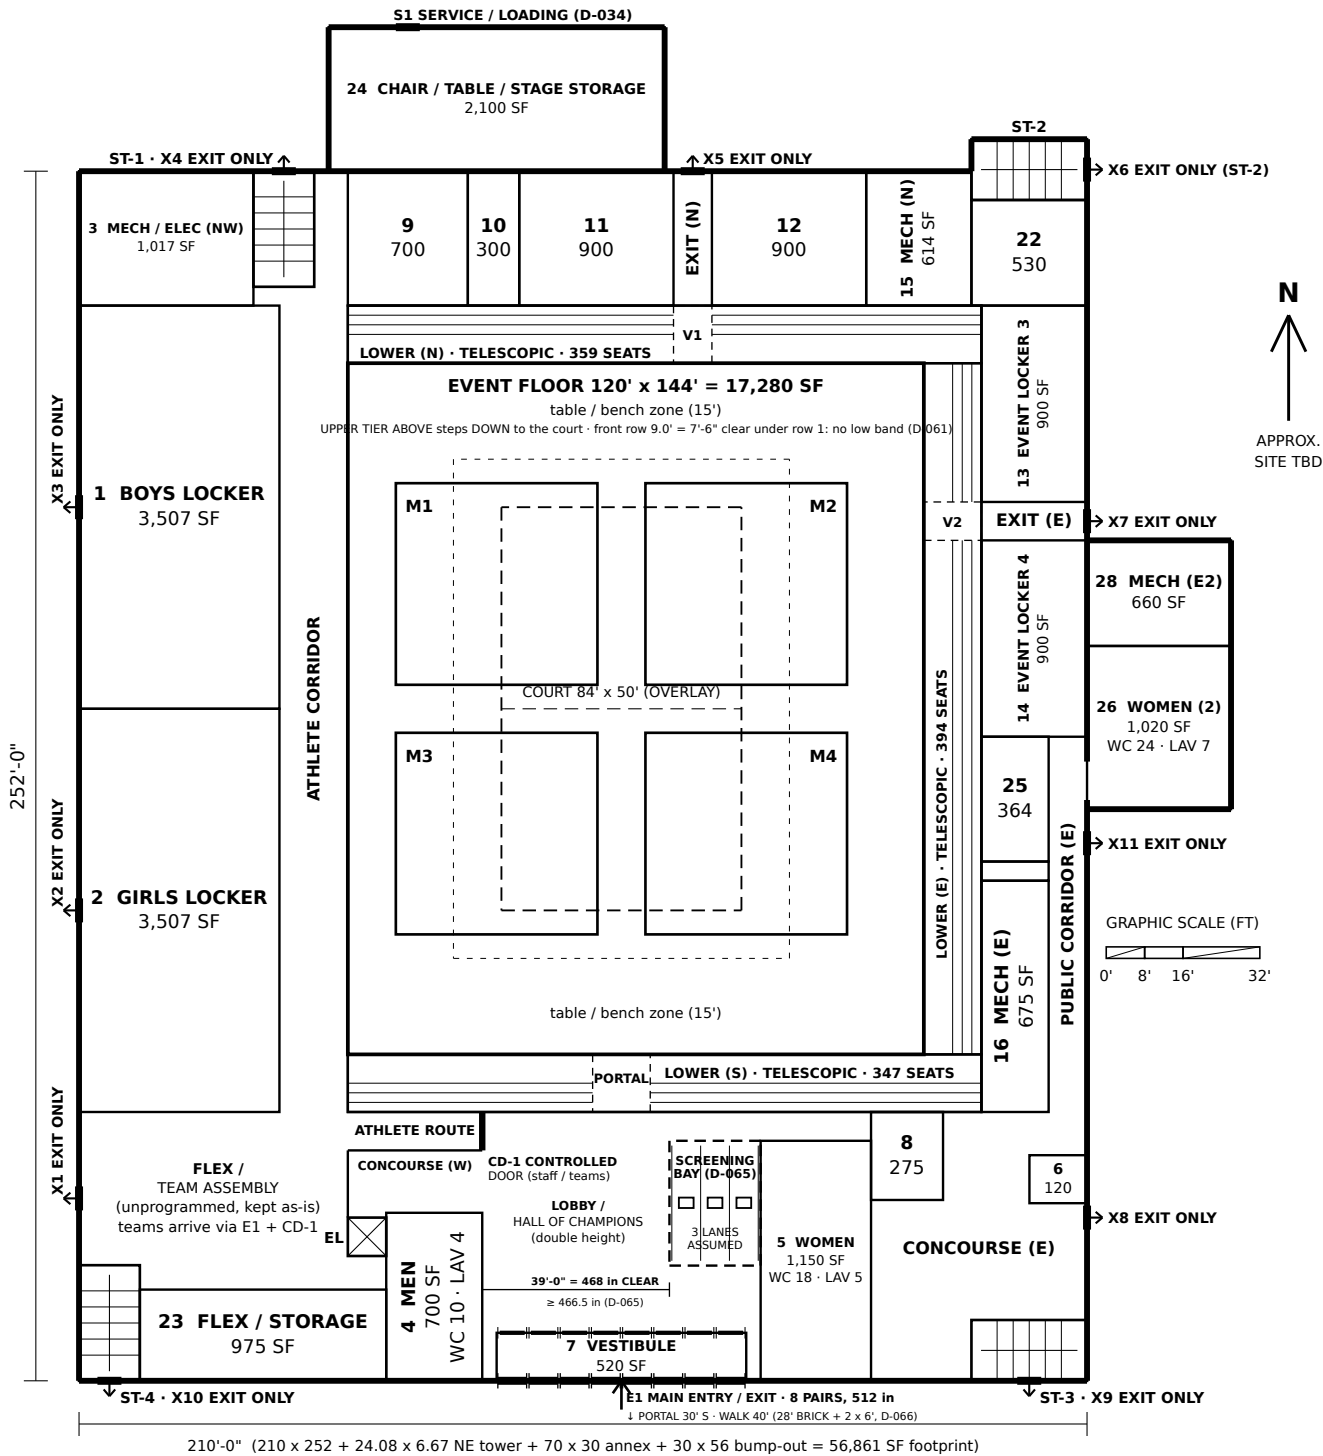

PRELIMINARY — CONCEPTUAL DESIGN — NOT FOR CONSTRUCTION

PROJECT	PHASE	SHEET TITLE	SCALE	DATE	REV	DRAWN BY	SHEET
Hazel Green Regional Athletic Complex Trojan Horse Arena · Hazel Green area, Madison County, Alabama (site TBD, D-006)	PHASE 2	OVERALL FLOOR PLAN LEVEL 1 · BLOCK PLAN	1" = 40'-0"	October 2026	J	Drawn by Claude (AI) for Shane Brazelton	P2-A-101