



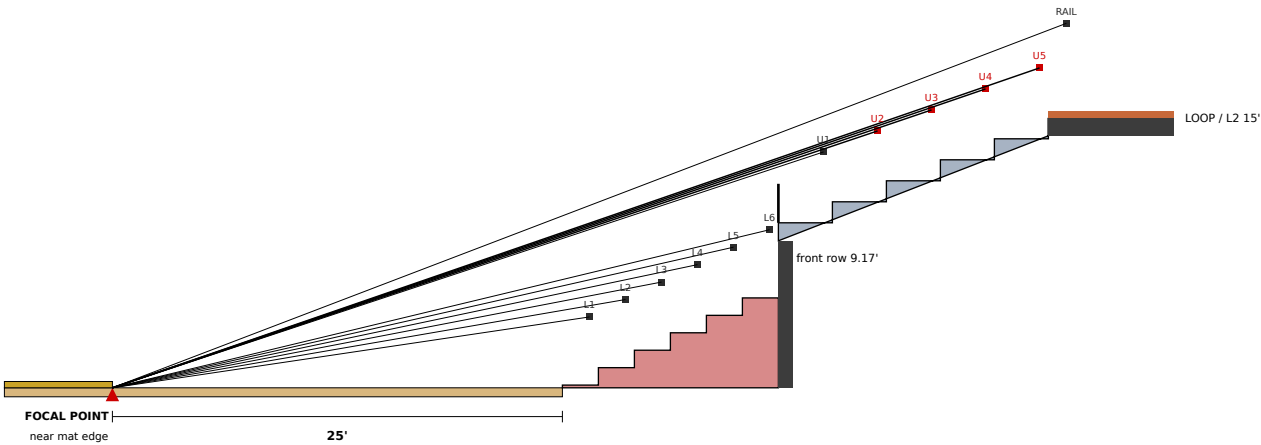


1 AS DRAWN — NORTH / SOUTH SIDE (seated eyes)

3/32" = 1'-0" · focal 25' (10' clear + 15' table zone) · telescopic 11½" · upper 14"/row

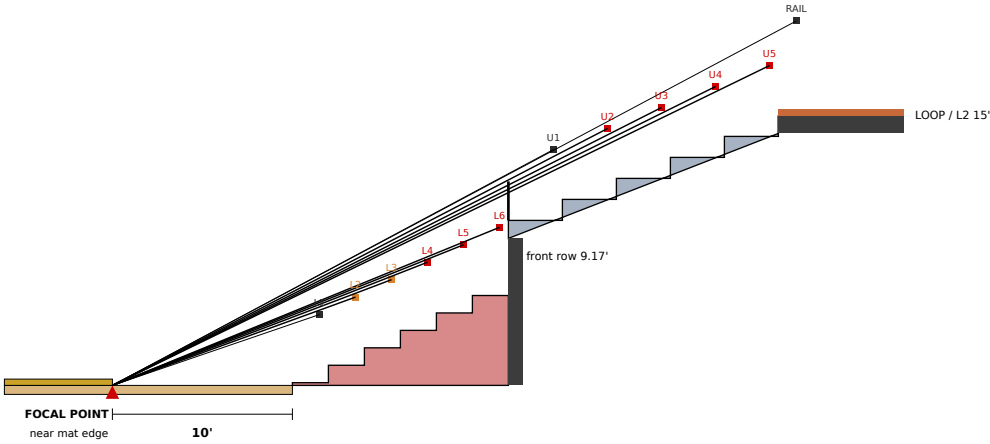

2 AS DRAWN — EAST SIDE (seated eyes)

3/32" = 1'-0" · focal 10' (10' clear) · worst side

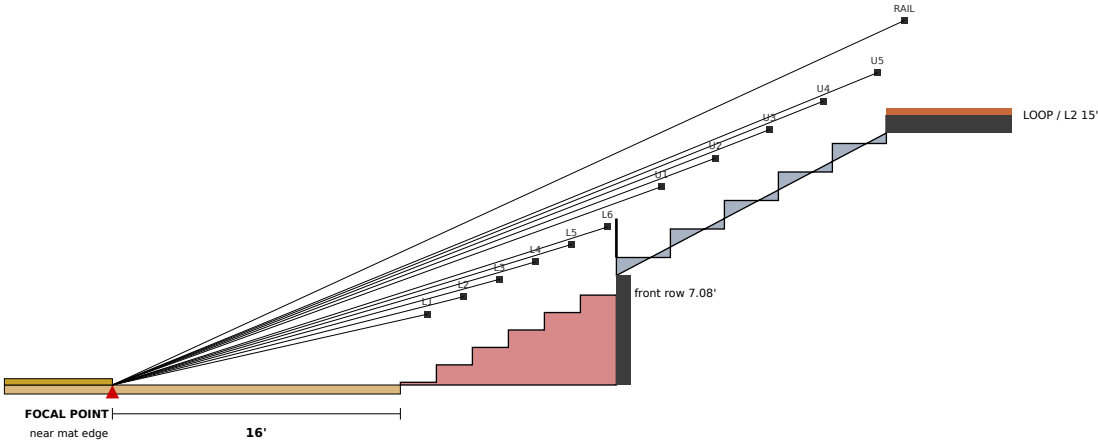

3 PROPOSED — EAST SIDE (seated eyes)

3/32" = 1'-0" · focal 16' (+6') · upper 19"/row, front 7.08' (D-053)


SIGHTLINE GRADE (C, mm)

- ≥ 90 PASS
- 60-90 MARGINAL
- < 60 FAIL

Dots = eyes; label colour = C of that row over the row in front. Values: table.

4 TELESCOPIC STACK UNDER THE UPPER-TIER FRONT

3/16" = 1'-0" · recessed (Hussey) · N/S as drawn · dashed = proposed 7.08' front

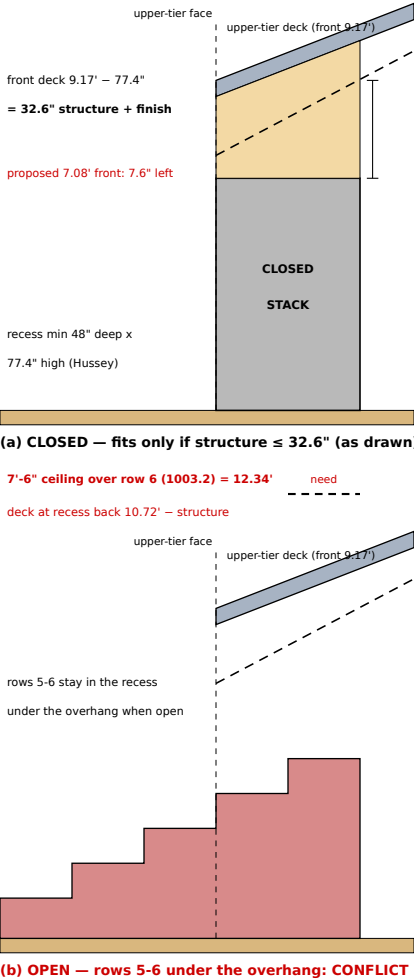

PRELIMINARY — CONCEPTUAL DESIGN — NOT FOR CONSTRUCTION

PROJECT	PHASE	SHEET TITLE	SCALE	DATE	REV	DRAWN BY	SHEET
Hazel Green Regional Athletic Complex Trojan Horse Arena · Hazel Green area, Madison County, Alabama (site TBD, D-006)	PHASE 2	SIGHT-LINE STUDY SCHEMATIC · COLOR	AS NOTED	October 2026	A	Drawn by KEYSTONE (AI) for Shane Brazelton	P2-A-302